ZSD č. 1 - SO 101 - PŮDORYS 1. NP

1 : 50

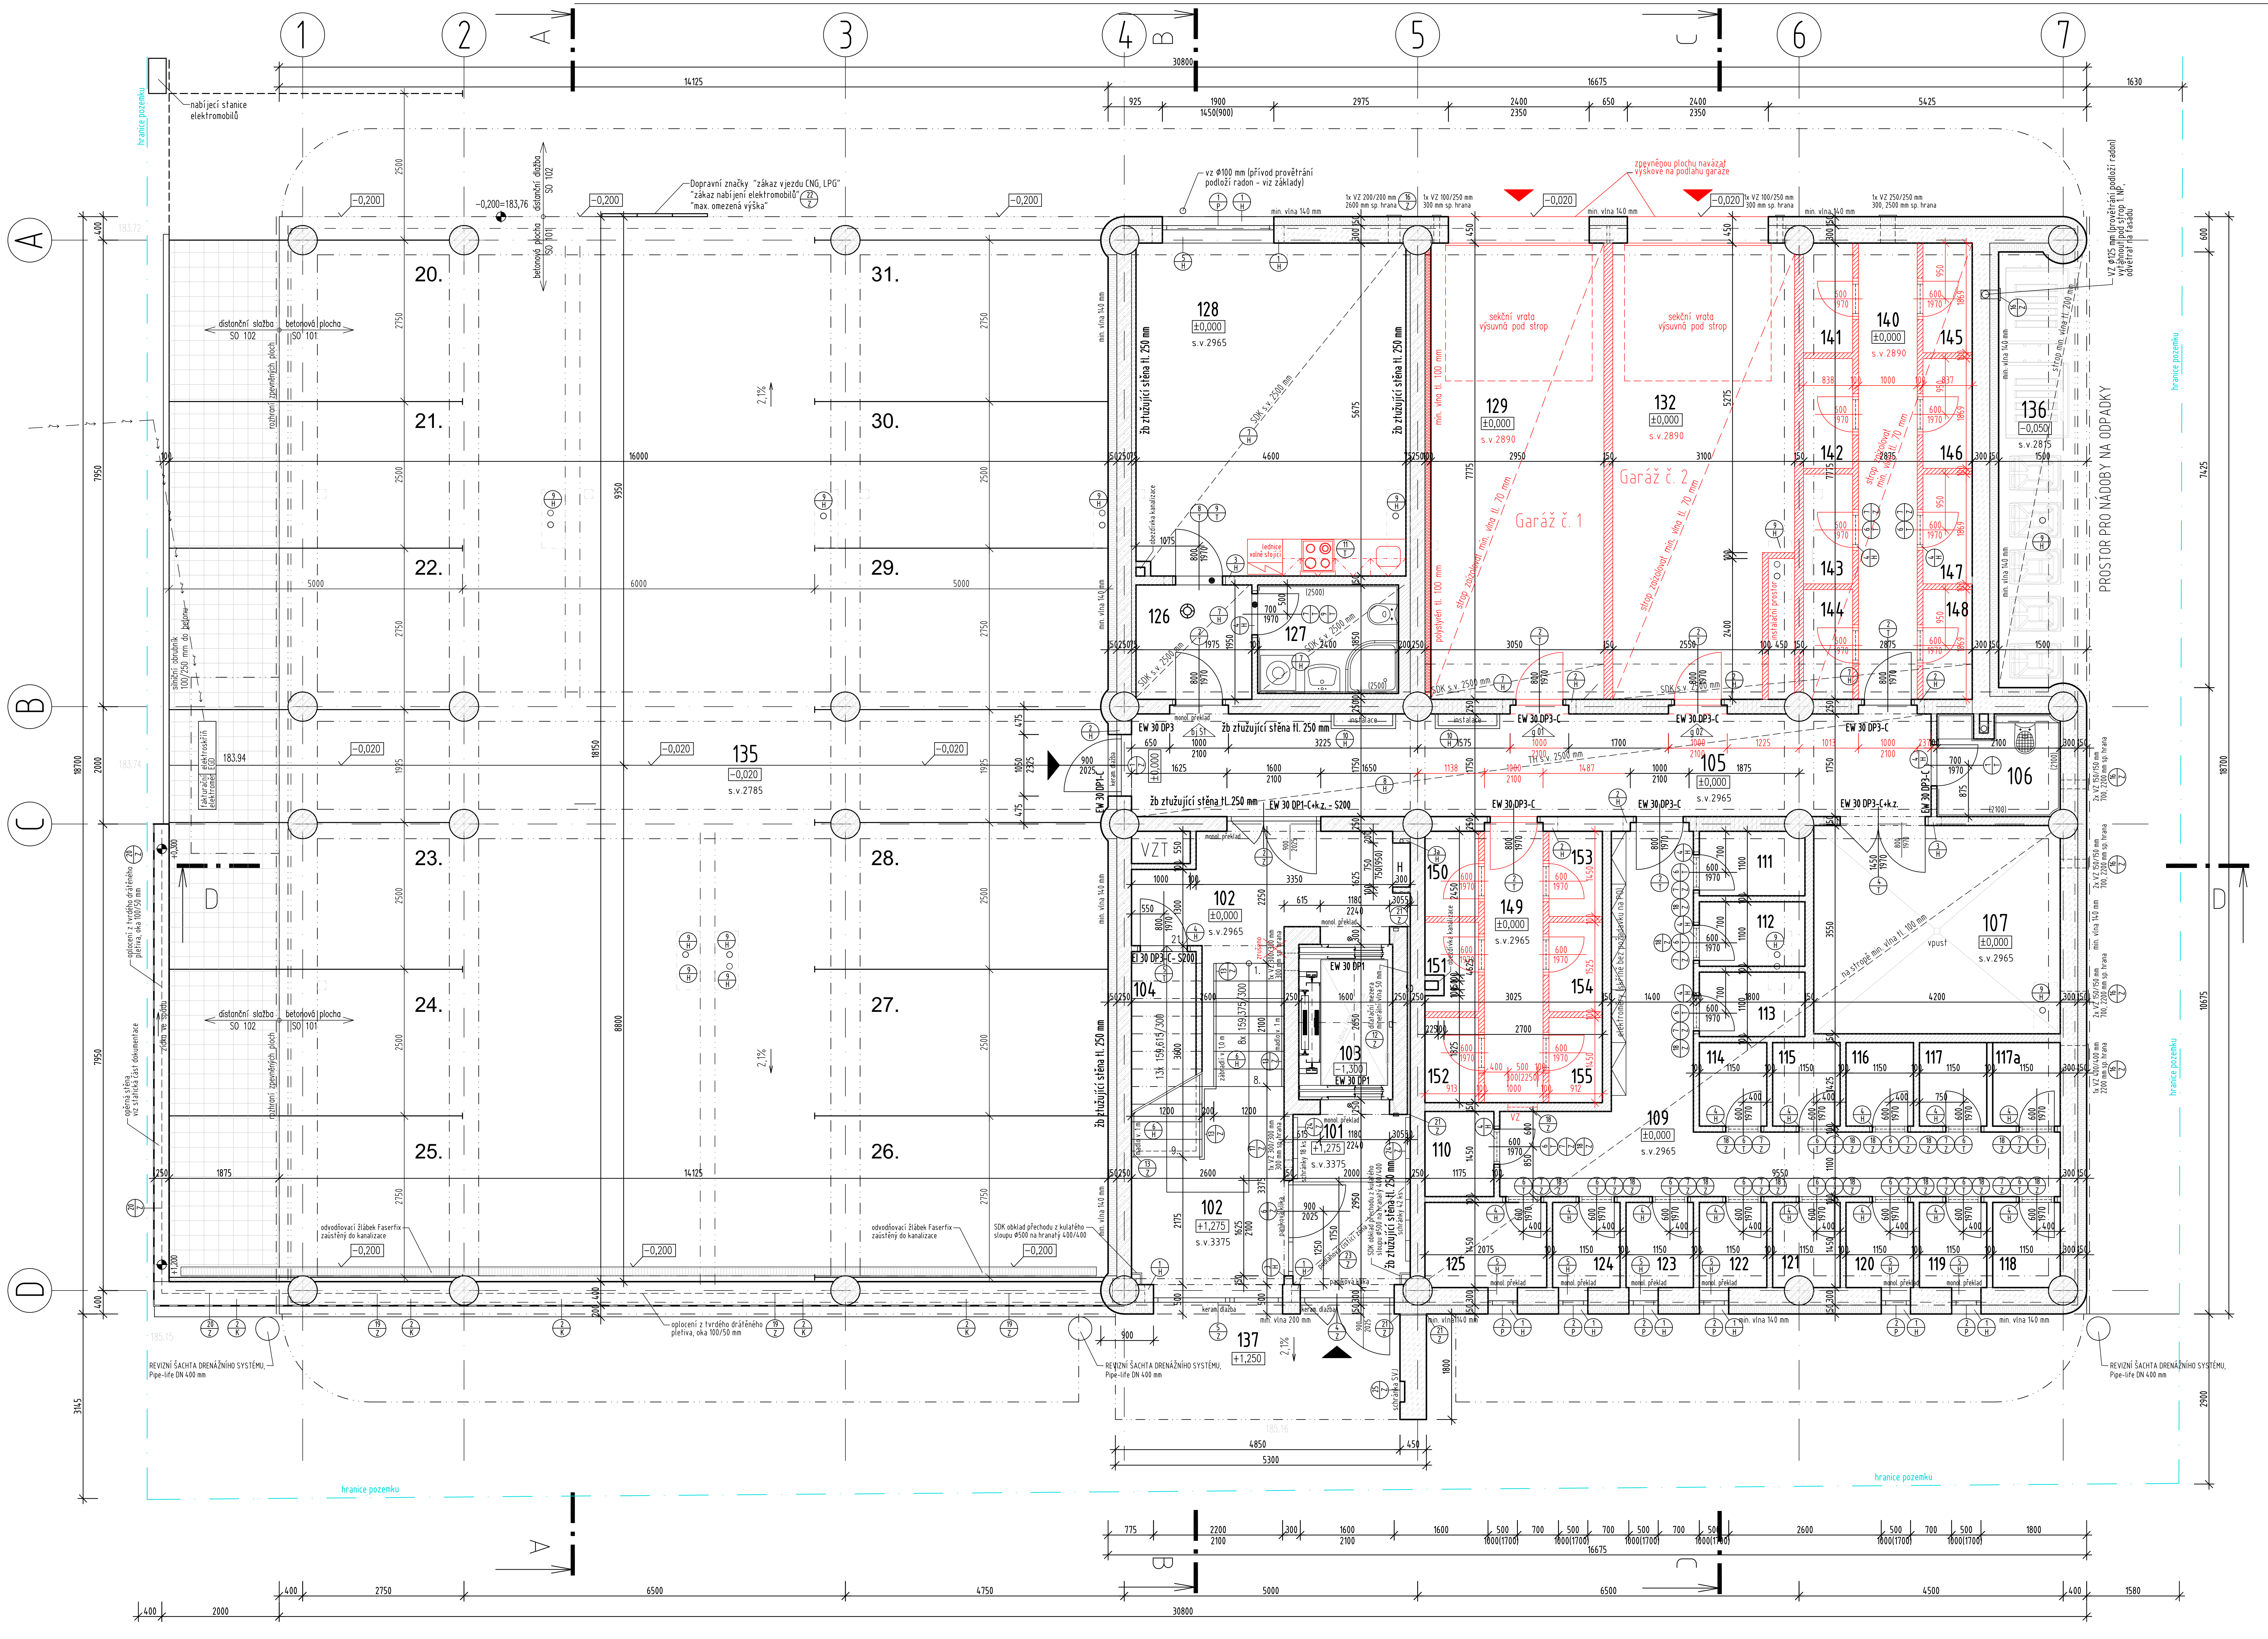

LEGENDA MÍSTNOSTÍ 1. NP

ČÍSLO	NÁZEV	PLOCHA[m2]	PODLAHA		STĚNY, STROP	POZNÁMKA
101	ZÁDVEŘÍ	6,15	KERAMICKÁ DLAŽBA	D	VOS, MJB	
102	SCHODIŠTĚ	19,20	KERAMICKÁ DLAŽBA	B,D	VOS, MJB	KERAMICKÉ STUPNĚ
103	VÝTAHOVÁ ŠACHTA	4,25	BETONOVÁ PODLAHA	F1	VOS, MJB	
104	ROZVADĚČ ČERPADLA KANALIZACE	3,75	KERAMICKÁ DLAŽBA	B	VOS, MJB	
105	CHODBA	24,35	KERAMICKÁ DLAŽBA	B	VOS, MJB, SDK	TH s.v. 2500 mm
106	ÚKLIDOVÁ KOMORA	3,50	KERAMICKÁ DLAŽBA	B	VOS, MJB, PO	PO v. 2100 mm
107	VÝMĚNÍKOVÁ STANICE	14.90	KERAMICKÁ DLAŽBA	B	VOS, MJB	STROP min. vlna tl. 100 mm
~~108~~	zrušeno	–	–	–	–	
109	CHODBA	17,10	KERAMICKÁ DLAŽBA	B	VOS, MJB	STROP min. vlna tl. 100 mm
110	Sklepní kóje č. 16	1,70	KERAMICKÁ DLAŽBA	B	VOS, MJB	STROP min. vlna tl. 100 mm
111	Sklepní kóje č. 1 (ústředna slaboproudu)	1,95	KERAMICKÁ DLAŽBA	B	VOS, MJB	STROP min. vlna tl. 100 mm
112	Sklepní kóje č. 2	2,00	KERAMICKÁ DLAŽBA	B	VOS, MJB	STROP min. vlna tl. 100 mm
113	Sklepní kóje č. 3	2,00	KERAMICKÁ DLAŽBA	B	VOS, MJB	STROP min. vlna tl. 100 mm
114	Sklepní kóje č. 4	1,65	KERAMICKÁ DLAŽBA	B	VOS, MJB	STROP min. vlna tl. 100 mm
115	Sklepní kóje č. 5	1,65	KERAMICKÁ DLAŽBA	B	VOS, MJB	STROP min. vlna tl. 100 mm
116	Sklepní kóje č. 6	1,65	KERAMICKÁ DLAŽBA	B	VOS, MJB	STROP min. vlna tl. 100 mm
117	Sklepní kóje č. 7	1,65	KERAMICKÁ DLAŽBA	B	VOS, MJB	STROP min. vlna tl. 100 mm
117a	Sklepní kóje č. 17	1,65	KERAMICKÁ DLAŽBA	B	VOS, MJB	STROP min. vlna tl. 100 mm
118	Sklepní kóje č. 8	1,65	KERAMICKÁ DLAŽBA	B	VOS, MJB	STROP min. vlna tl. 100 mm
119	Sklepní kóje č. 9	1,65	KERAMICKÁ DLAŽBA	B	VOS, MJB	STROP min. vlna tl. 100 mm
120	Sklepní kóje č. 10	1,65	KERAMICKÁ DLAŽBA	B	VOS, MJB	STROP min. vlna tl. 100 mm
121	Sklepní kóje č. 11	1,55	KERAMICKÁ DLAŽBA	B	VOS, MJB	STROP min. vlna tl. 100 mm
122	Sklepní kóje č. 12	1,65	KERAMICKÁ DLAŽBA	B	VOS, MJB	STROP min. vlna tl. 100 mm
123	Sklepní kóje č. 13	1,65	KERAMICKÁ DLAŽBA	B	VOS, MJB	STROP min. vlna tl. 100 mm
124	Sklepní kóje č. 14 (hlavní uzávěr vody)	1,65	KERAMICKÁ DLAŽBA	B	VOS, MJB	STROP min. vlna tl. 100 mm
125	Sklepní kóje č. 15	3,00	KERAMICKÁ DLAŽBA	B	VOS, MJB	STROP min. vlna tl. 100 mm
	BYTOVÁ JEDNOTKA č. 51 (plocha : 34,40 m2)					
126	PŘEDSÍŇ	3,85	VINYL tl. 3 mm (lepený)	C	VOS, MJB, SDK	SDK s.v. 2500 mm
127	KOUPELNA, WC	4,45	KERAMICKÁ DLAŽBA	A	VOS, MJB, PO, SDK	SDK s.v. 2500 mm PO v. 2500 mm
128	POKOJ + KK	26,10	VINYL tl. 3 mm (lepený)	C	VOS, MJB, SDK	SDK s.v. 2500 mm
	GARÁŽ č. 1 (plocha : 22,90 m2)					
129	GARÁŽ	22,90	BETONOVÁ PODLAHA + NÁTĚR	–	VOS, MJB, SDK	SDK s.v. 2500 mm
~~130~~	zrušeno	–	–	–	–	–
~~131~~	zrušeno	–	–	–	–	–
	Garáž č. 2 (plocha : 22,70 m2)					
132	GARÁŽ	22,70	BETONOVÁ PODLAHA + NÁTĚR	–	VOS, MJB, SDK	SDK s.v. 2500 mm
~~133~~	zrušeno	–	–	–	–	–
~~134~~	zrušeno	–	–	–	–	–
	Venkovní prostor					
135	Parkovací stání (12 OA)	256,30	BET. POJÍZDNÁ PLOCHA tl. 250 mm	E	VIZ FASÁDA	STROP min. vlna tl. 200 mm
136	Prostor pro nádoby na odpady	11,05	ZÁMKOVÁ DLAŽBA tl. 60 mm	G1	VIZ FASÁDA	STROP min. vlna tl. 200 mm
137	Přestřešený venkovní vstup	9,00	ZÁMKOVÁ DLAŽBA tl. 60 mm	–	VIZ FASÁDA	součást SO 102
	Doplnění sklepních kójí					
140	CHODBA	7,80	KERAMICKÁ DLAŽBA	B	VOS, MJB	STROP min. vlna tl. 70 mm
141	Sklepní kóje č. 18	1,55	KERAMICKÁ DLAŽBA	B	VOS, MJB	STROP min. vlna tl. 70 mm
142	Sklepní kóje č. 19	1,55	KERAMICKÁ DLAŽBA	B	VOS, MJB	STROP min. vlna tl. 70 mm
143	Sklepní kóje č. 20	1,55	KERAMICKÁ DLAŽBA	B	VOS, MJB	STROP min. vlna tl. 70 mm
144	Sklepní kóje č. 21	1,55	KERAMICKÁ DLAŽBA	B	VOS, MJB	STROP min. vlna tl. 70 mm
145	Sklepní kóje č. 22	1,55	KERAMICKÁ DLAŽBA	B	VOS, MJB	STROP min. vlna tl. 70 mm
146	Sklepní kóje č. 23	1,55	KERAMICKÁ DLAŽBA	B	VOS, MJB	STROP min. vlna tl. 70 mm
147	Sklepní kóje č. 24	1,55	KERAMICKÁ DLAŽBA	B	VOS, MJB	STROP min. vlna tl. 70 mm
148	Sklepní kóje č. 25	1,55	KERAMICKÁ DLAŽBA	B	VOS, MJB	STROP min. vlna tl. 70 mm
	Doplnění sklepních kójí					
149	CHODBA	4,80	KERAMICKÁ DLAŽBA	B	VOS, MJB	STROP min. vlna tl. 100 mm
150	Sklepní kóje č. 26	1,30	KERAMICKÁ DLAŽBA	B	VOS, MJB	STROP min. vlna tl. 100 mm
151	Sklepní kóje č. 27	1,30	KERAMICKÁ DLAŽBA	B	VOS, MJB	STROP min. vlna tl. 100 mm
152	Sklepní kóje č. 28	1,30	KERAMICKÁ DLAŽBA	B	VOS, MJB	STROP min. vlna tl. 100 mm
153	Sklepní kóje č. 29	1,30	KERAMICKÁ DLAŽBA	B	VOS, MJB	STROP min. vlna tl. 100 mm
154	Sklepní kóje č. 30	1,40	KERAMICKÁ DLAŽBA	B	VOS, MJB	STROP min. vlna tl. 100 mm
155	Sklepní kóje č. 31	1,30	KERAMICKÁ DLAŽBA	B	VOS, MJB	STROP min. vlna tl. 100 mm

POZNÁMKA:

VOS	VÁPENNÁ OMÍTKA ŠTUKOVÁ	PO	PÓROVINOVÝ OBKLAD	TH	PODHLED THERMATEX 600/600 mm (8/T)
MJB	MALBA JEDNOBAREVNÁ BÍLÁ	SDK	SÁDROKARTONOVÝ PODHLED (7/T)		

● MŘÍŽKY DO DVEŘÍ 400/80 mm vřezané ke spodní hraně dveří (v místnostech sociálních zařízení s podtlakovým větráním) -12/T

LEGENDA ZDIVA 1. NP

○ ▨	ŽELEZOBETONOVÉ MONOLITICKÉ NOSNÉ KONSTRUKCE (sloupy ø500, 400/400 mm, pilíře, stropní desky, ztužující stěny, opěrné stěny, výtahová šachta) SOUČÁST STATICKÉ ČÁSTI DOKUMENTACE
▨	ODBODOVÉ VÝPLŇOVÉ ZDIVO Z BROUŠENÝCH BLOKŮ POROTHERM 30 PROFI (247x300x249 mm) tl. 300 mm PEVNOSTI P15 VYZDÍVANÉ NA MALTU PRO TENKÉ SPÁRY (na zdivu proveden kontaktní zateplovací systém s min. vlnou tl. 200 mm, ostění otvorů zatepleno min. vlnou tl. min. 30 mm)
▨	MEZIBYTOVÉ STĚNY Z BLOKŮ Cihla Porotherm 25 AKU SYM – Akustická P 15 (rozměr 372 x 238 x 250 mm) tl. 250 mm, akustický cihelný blok s maltovou kapsou pro tl. stěny 25 cm na maltu M 10. Cihly jsou velmi vhodné pro mezibytové příčky tloušťky 250 mm. ZVUKOVÁ IZOLACE ZDIVA Rw = 57 dB (plošná hm. zdiva včetně omítek min. 313 kg/m2)
▨	ZDIVO PŘÍČEK Z PŘÍČKOVEK PORFIX TL. 100 mm a 150 mm a 200 mm VYZDÍVANÉ NA TMEL PORFIX (příčky, přizdívky), OMÍTKY VYZTUŽIT PERLINKOU

SEZNAM STAVEBNÍCH ÚPRAV :

18/Z	VĚTRACÍ OTVORY NAD VSTUPNÍMI DVEŘMI DO SKLEPNÍCH KÓJÍ. Rozměr 500 x 300 mm. Spodní hrana 2250 mm. VÝPLŇ Tahokov z ocelového plechu TR 28 x 9 x 2 mm, 1,5x1000x2000 mm, délka oka 28 mm – celkem 32 ks.
◎	ZAŘÍZENÍ AUTONOMNÍ DETEKCE a SIGNALIZACE POŽÁRU (dle PBŘ stavby)

POZNÁMKA :

STROPY V OBYTNÝCH I NEOBYTNÝCH MÍSTNOSTECH BYTOVÝCH JEDNOTEK MOHOU BÝT OPATŘENY SDK PODHLEDY na s.v. 2,54 m (DLE VYHL. 146/2024 SB. min s.v. = 2,50 m)

±0,000 = PODLAHA 1. NP = 183,960 m.n.m., výškový systém B.p.V.

ZMĚNA STAVBY PŘED DOKONČENÍM č. 1

VEDOUCÍ PROJEKTANT	VYPRACOVAL	OBJEKT SO-101	PROJEKTOVÁ KANCELÁŘ FABEDI s.r.o.
ING. ARCH. RADKO PAVLACKÝ	ING. MICHAL NÁJEMNÍK	APARTMÁNOVÝ-bytový DŮM	Nám.3. května 1605 765 02 Otrokovice IČ: 116 78 852

INVESTOR: KŘETÍNSKÝ INVEST s.r.o., nám. 3. května 1820, 765 02 Otrokovice, IČO: 037 96 884

APARTMÁNOVÝ - BYTOVÝ DŮM V OTROKOVICÍCH
parc. č.st. 2120, 439/175, 439/117, 439/88, k.ú. Otrokovice
D.1.1 - ARCHITEKTONICKO - STAVEBNÍ ŘEŠENÍ

DATUM	09. 2026
FORMÁT	10 x A4
STUPEŇ	ZSD č. 1
ZAK. ČÍSLO	25 - 01
MĚŘÍTKO	1 : 50

PŮDORYS 1. NP | ZSD č. 1 | D 1.1 | 101/05