ZSD č. 1 – SO 101 – PŮDORYS 2. NP

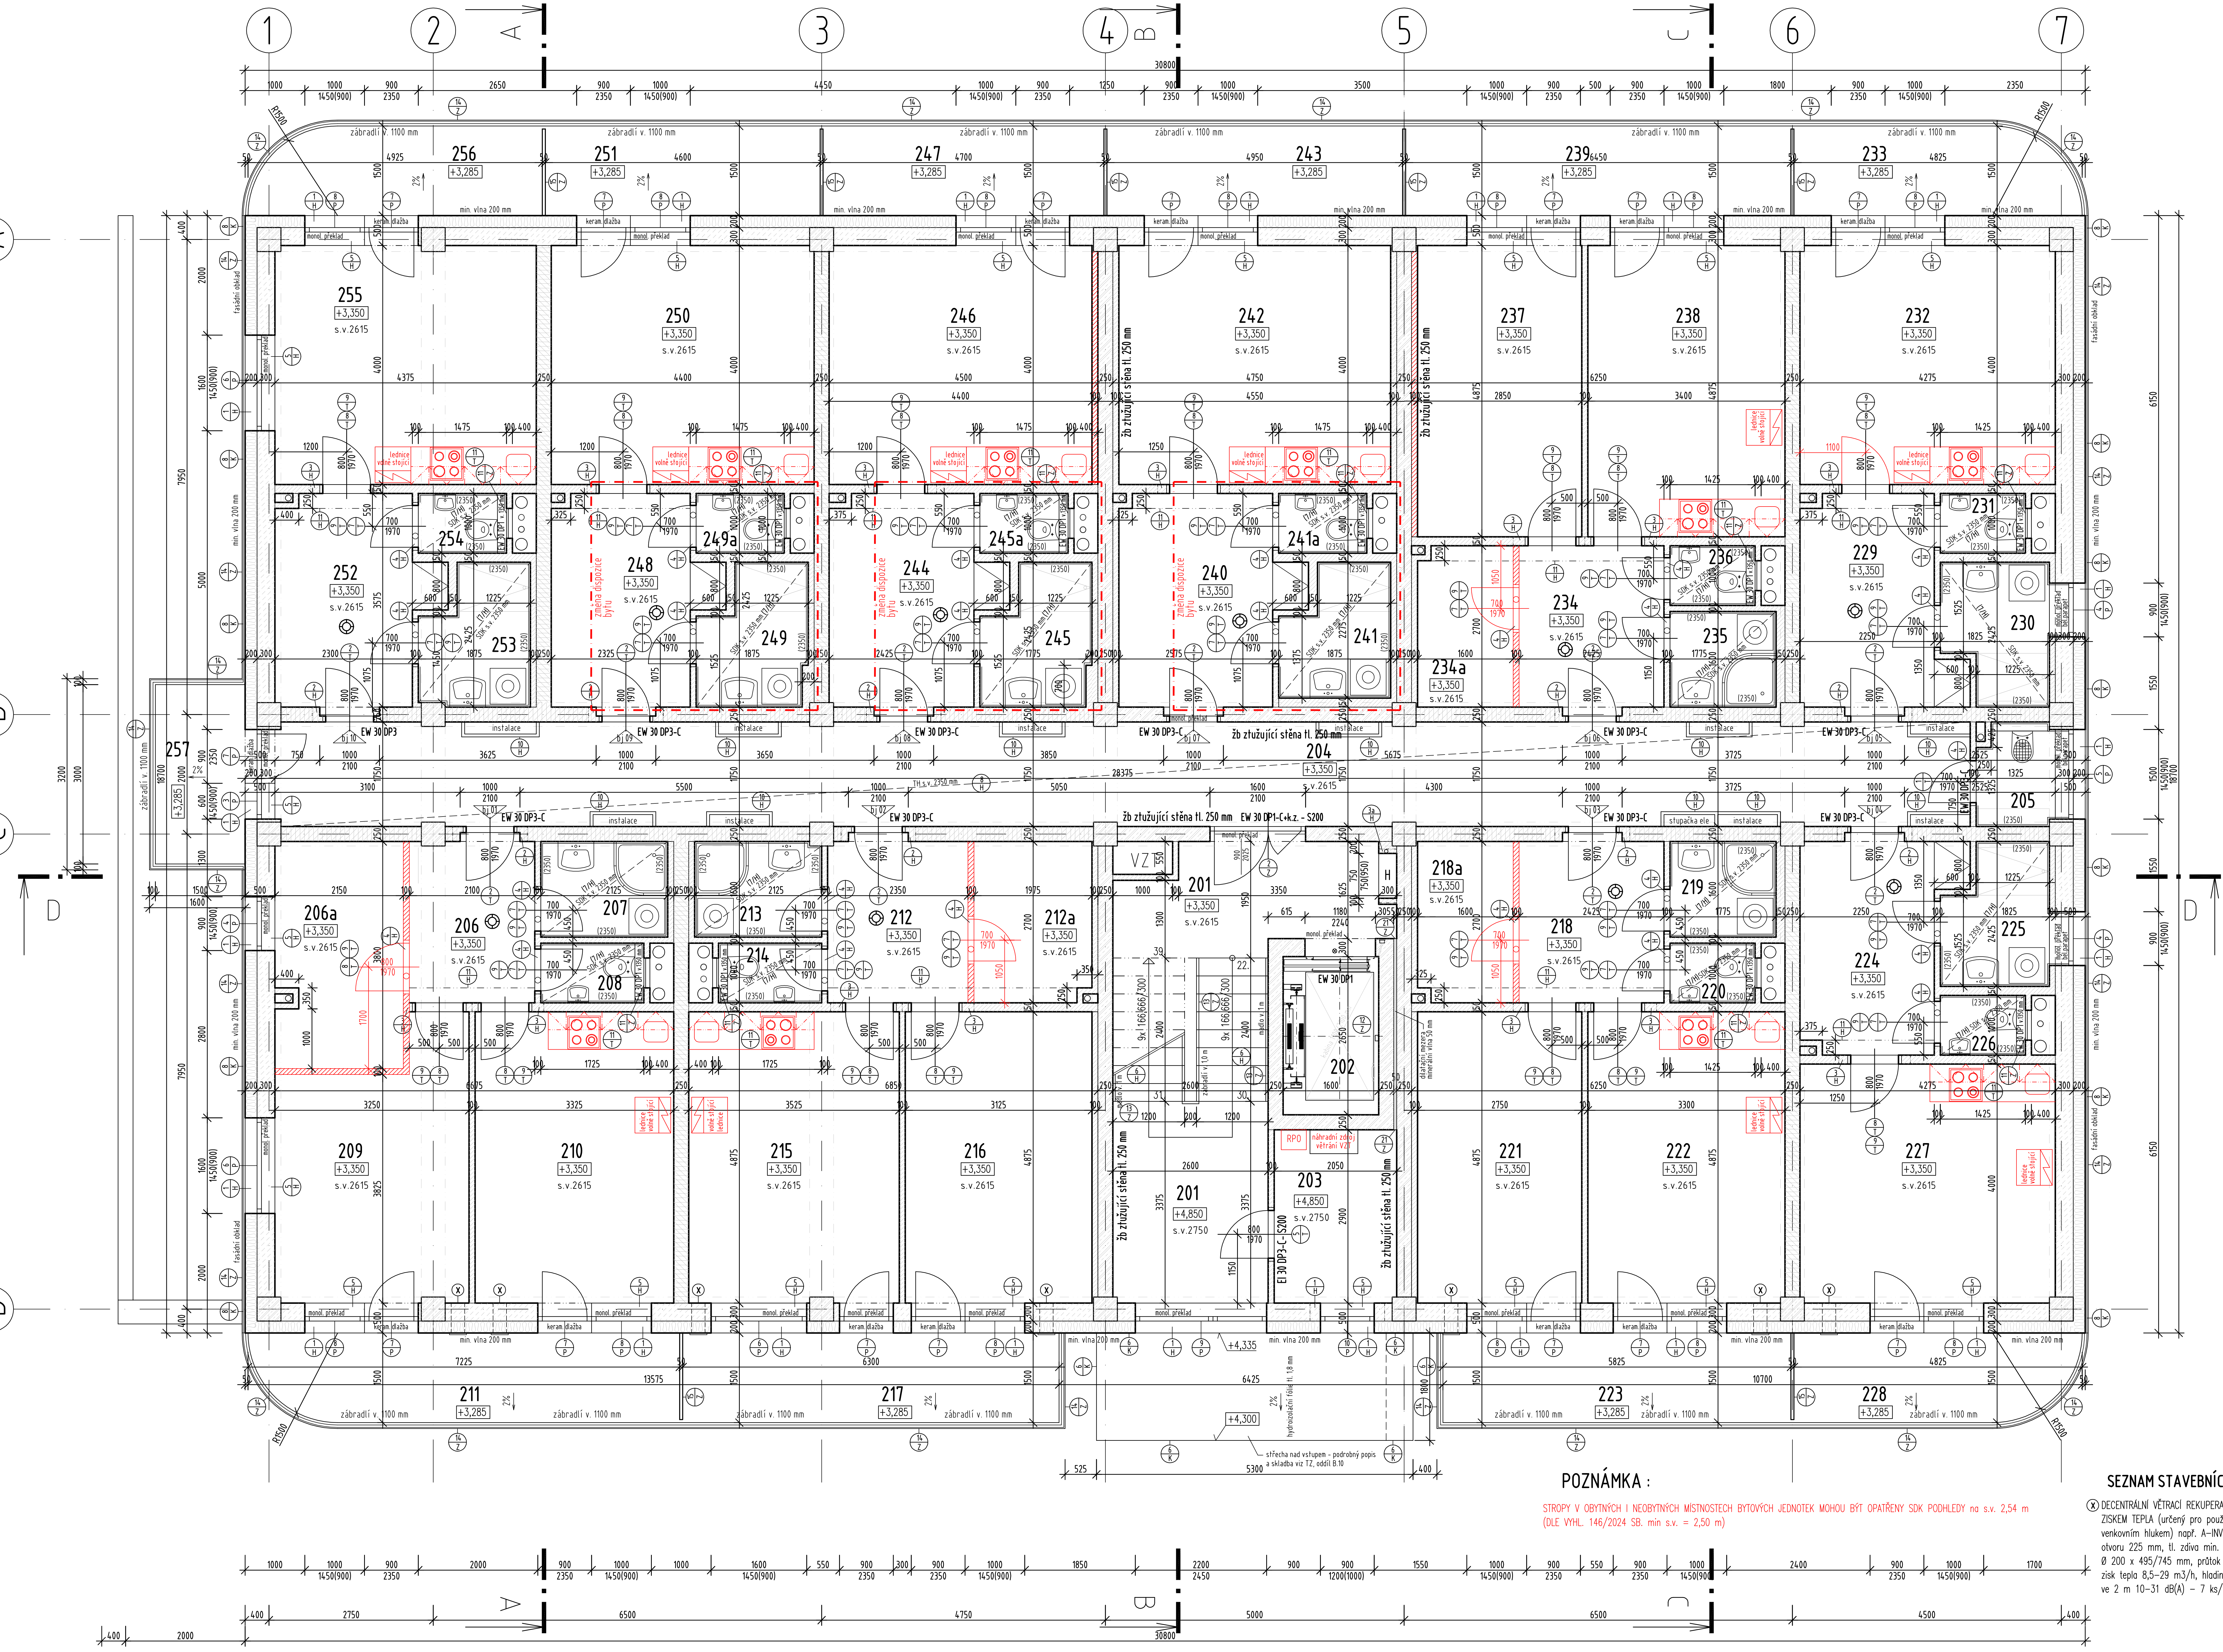

LEGENDA ZDIVA 2. NP

- ▨ ŽELEZOBETONOVÉ MONOLITICKÉ NOSNÉ KONSTRUKCE (sloupy ø500, 400/400 mm, pilíře, stropní desky, ztužující stěny, opěrné stěny, výtahová šachta) SOUČÁST STATICKÉ ČÁSTI DOKUMENTACE
- ▨ ODBODOVÉ VÝPLŇOVÉ ZDIVO Z BROUŠENÝCH BLOKŮ POROTHERM 30 PROFI (247x300x249 mm) tl. 300 mm PEVNOSTI P15 VYZDÍVANÉ NA MALTU PRO TENKÉ SPÁRY (na zdivu proveden kontaktní zateplovací systém s min. vlnou tl. 200 mm, ostění otvorů zatepleno min. vlnou tl. min. 30 mm)
- ▨ MEZIBYTOVÉ STĚNY Z BLOKŮ Cihla Porotherm 25 AKU SYM – Akustická P 15 (rozměr 372 x 238 x 250 mm) tl. 250 mm, akustický cihelný blok s maltovou kapsou pro tl. stěny 25 cm na maltu M 10. Cihly jsou velmi vhodné pro mezibytové příčky tloušťky 250 mm. ZVUKOVÁ IZOLACE ZDIVA Rw = 57 dB (plošná hm. zdiva včetně omítek min. 313 kg/m2)
- ▨ ZDIVO PŘÍČEK Z PŘÍČKOVEK PORFIX TL. 100 mm, 150 mm a 200 mm VYZDÍVANÉ NA TMEL PORFIX (příčky, přizdívky), OMÍTKY VYZTUŽIT PERLINKOU
- ○ MŘÍŽKY DO DVEŘÍ 400/80 mm vřezané ke spodní hraně dveří (v místnostech sociálních zařízení s podtlakovým větráním) -12/T

LEGENDA MÍSTNOSTÍ 2. NP

1 : 50

ČÍSLO	NÁZEV	PLOCHA[m2]	PODLAHA		STĚNY, STROP	POZNÁMKA
201	SCHODIŠTĚ	22,55	KERAMICKÁ DLAŽBA	D,E1	VOS, MJB	KERAMICKÉ STUPNĚ
202	VÝTAHOVÁ ŠACHTA	4,25	BETONOVÁ PODLAHA	x	VOS, MJB	
203	NÁHRADNÍ ZDROJ VZT	5,95	KERAMICKÁ DLAŽBA	D	VOS, MJB	
204	CHODBA	49,30	KERAMICKÁ DLAŽBA	E1	VOS, MJB	TH s.v. 2350 mm
205	ÚKLIDOVÁ KOMORA	2,20	KERAMICKÁ DLAŽBA	E1	VOS, MJB, PO	PO v. 2100 mm
BYTOVÁ JEDNOTKA č. 1 (plocha : 48,85 m2 + balkon 10,35 m2)						
206	PŘEDSÍŇ	5,65	VINYL tl. 3 mm (lepený)	G	VOS, MJB	
206a	KOMORA	8,05	VINYL tl. 3 mm (lepený)	G	VOS, MJB	
207	KOUPELNA	3,40	KERAMICKÁ DLAŽBA	F	VOS, MJB, PO, SDK	SDK s.v. 2350 mm PO v. 2350 mm
208	WC	1,75	KERAMICKÁ DLAŽBA	F	VOS, MJB, PO, SDK	SDK s.v. 2350 mm PO v. 2350 mm
209	POKOJ	13,40	VINYL tl. 3 mm (lepený)	G	VOS, MJB	
210	POKOJ + KK	16,60	VINYL tl. 3 mm (lepený)	G	VOS, MJB	
211	BALKON	10,35	DLAŽBA NA TERČÍCH	H	viz fasáda	
BYTOVÁ JEDNOTKA č. 2 (plocha : 49,85 m2 + balkon 9,45 m2)						
212	PŘEDSÍŇ	6,35	VINYL tl. 3 mm (lepený)	G	VOS, MJB	
212a	KOMORA	5,25	VINYL tl. 3 mm (lepený)	G	VOS, MJB	
213	KOUPELNA	3,40	KERAMICKÁ DLAŽBA	F	VOS, MJB, PO, SDK	SDK s.v. 2350 mm PO v. 2350 mm
214	WC	1,75	KERAMICKÁ DLAŽBA	F	VOS, MJB, PO, SDK	SDK s.v. 2350 mm PO v. 2350 mm
215	POKOJ + KK	17,50	VINYL tl. 3 mm (lepený)	G	VOS, MJB	
216	POKOJ	15,60	VINYL tl. 3 mm (lepený)	G	VOS, MJB	
217	BALKON	9,45	DLAŽBA NA TERČÍCH	H	viz fasáda	
BYTOVÁ JEDNOTKA č. 3 (plocha : 44,95 m2 + balkon 8,75 m2)						
218	PŘEDSÍŇ	6,55	VINYL tl. 3 mm (lepený)	G	VOS, MJB	
218a	KOMORA	4,25	VINYL tl. 3 mm (lepený)	G	VOS, MJB	
219	KOUPELNA	2,80	KERAMICKÁ DLAŽBA	F	VOS, MJB, PO, SDK	SDK s.v. 2350 mm PO v. 2350 mm
220	WC	1,45	KERAMICKÁ DLAŽBA	F	VOS, MJB, PO, SDK	SDK s.v. 2350 mm PO v. 2350 mm
221	POKOJ	13,60	VINYL tl. 3 mm (lepený)	G	VOS, MJB	
222	POKOJ + KK	16,30	VINYL tl. 3 mm (lepený)	G	VOS, MJB	
223	BALKON	8,75	DLAŽBA NA TERČÍCH	H	viz fasáda	
BYTOVÁ JEDNOTKA č. 4 (plocha : 31,25 m2 + balkon 6,75 m2)						
224	PŘEDSÍŇ, KUCHYNĚ	8,60	VINYL tl. 3 mm (lepený)	G	VOS, MJB	
225	KOUPELNA	3,90	KERAMICKÁ DLAŽBA	F	VOS, MJB, PO, SDK	SDK s.v. 2350 mm PO v. 2350 mm
226	WC	1,45	KERAMICKÁ DLAŽBA	F	VOS, MJB, PO, SDK	SDK s.v. 2350 mm PO v. 2350 mm
227	POKOJ + KK	17,30	VINYL tl. 3 mm (lepený)	G	VOS, MJB	
228	BALKON	6,75	DLAŽBA NA TERČÍCH	H	viz fasáda	
BYTOVÁ JEDNOTKA č. 5 (plocha : 31,25 m2 + balkon 6,75 m2)						
229	PŘEDSÍŇ	8,60	VINYL tl. 3 mm (lepený)	G	VOS, MJB	
230	KOUPELNA	3,90	KERAMICKÁ DLAŽBA	F	VOS, MJB, PO, SDK	SDK s.v. 2350 mm PO v. 2350 mm
231	WC	1,45	KERAMICKÁ DLAŽBA	F	VOS, MJB, PO, SDK	SDK s.v. 2350 mm PO v. 2350 mm
232	POKOJ + KK	17,30	VINYL tl. 3 mm (lepený)	G	VOS, MJB	
233	BALKON	6,75	DLAŽBA NA TERČÍCH	H	viz fasáda	
BYTOVÁ JEDNOTKA č. 6 (plocha : 44,95 m2 + balkon 9,70 m2) (plocha : 44,95 m2 + balkon 8,35 m2)						
234	PŘEDSÍŇ	6,55	VINYL tl. 3 mm (lepený)	G	VOS, MJB	
234a	KOMORA	4,25	VINYL tl. 3 mm (lepený)	G	VOS, MJB	
235	KOUPELNA	2,80	KERAMICKÁ DLAŽBA	F	VOS, MJB, PO, SDK	SDK s.v. 2350 mm PO v. 2350 mm
236	WC	1,45	KERAMICKÁ DLAŽBA	F	VOS, MJB, PO, SDK	SDK s.v. 2350 mm PO v. 2350 mm
237	POKOJ	13,60	VINYL tl. 3 mm (lepený)	G	VOS, MJB	
238	POKOJ + KK	16,30	VINYL tl. 3 mm (lepený)	G	VOS, MJB	
239	BALKON	9,70	DLAŽBA NA TERČÍCH	H	viz fasáda	
BYTOVÁ JEDNOTKA č. 7 (plocha : 32,90 m2 + balkon 7,40 m2)						
240	PŘEDSÍŇ	9,30	VINYL tl. 3 mm (lepený)	G	VOS, MJB	
241	KOUPELNA	3,70	KERAMICKÁ DLAŽBA	F	VOS, MJB, PO, SDK	SDK s.v. 2350 mm PO v. 2350 mm
241a	WC	1,50	KERAMICKÁ DLAŽBA	F	VOS, MJB, PO, SDK	SDK s.v. 2350 mm PO v. 2350 mm
242	POKOJ	18,40	VINYL tl. 3 mm (lepený)	G	VOS, MJB	
243	BALKON	7,40	DLAŽBA NA TERČÍCH	H	viz fasáda	
BYTOVÁ JEDNOTKA č. 8 (plocha : 31,85 m2 + balkon 7,05 m2)						
244	PŘEDSÍŇ	8,70	VINYL tl. 3 mm (lepený)	G	VOS, MJB	
245	KOUPELNA	3,85	KERAMICKÁ DLAŽBA	F	VOS, MJB, PO, SDK	SDK s.v. 2350 mm PO v. 2350 mm
245a	WC	1,50	KERAMICKÁ DLAŽBA	F	VOS, MJB, PO, SDK	SDK s.v. 2350 mm PO v. 2350 mm
246	POKOJ	17,80	VINYL tl. 3 mm (lepený)	G	VOS, MJB	
247	BALKON	7,05	DLAŽBA NA TERČÍCH	H	viz fasáda	
BYTOVÁ JEDNOTKA č. 9 (plocha : 31,55 m2 + balkon 6,90 m2)						
248	PŘEDSÍŇ	8,40	VINYL tl. 3 mm (lepený)	G	VOS, MJB	
249	KOUPELNA	3,85	KERAMICKÁ DLAŽBA	F	VOS, MJB, PO, SDK	SDK s.v. 2350 mm PO v. 2350 mm
249a	WC	1,50	KERAMICKÁ DLAŽBA	F	VOS, MJB, PO, SDK	SDK s.v. 2350 mm PO v. 2350 mm
250	POKOJ + KK	17,80	VINYL tl. 3 mm (lepený)	G	VOS, MJB	
251	BALKON	6,90	DLAŽBA NA TERČÍCH	H	viz fasáda	
BYTOVÁ JEDNOTKA č. 10 (plocha : 31,80 m2 + balkon 6,90 m2)						
252	PŘEDSÍŇ	8,75	VINYL tl. 3 mm (lepený)	G	VOS, MJB	
253	KOUPELNA	3,90	KERAMICKÁ DLAŽBA	F	VOS, MJB, PO, SDK	SDK s.v. 2350 mm PO v. 2350 mm
254	WC	1,50	KERAMICKÁ DLAŽBA	F	VOS, MJB, PO, SDK	SDK s.v. 2350 mm PO v. 2350 mm
255	POKOJ + KK	17,65	VINYL tl. 3 mm (lepený)	G	VOS, MJB	
256	BALKON	6,90	DLAŽBA NA TERČÍCH	H	viz fasáda	
257	BALKON	4,50	DLAŽBA NA TERČÍCH	H	viz fasáda	

POZNÁMKA: VOS VÁPENNÁ OMÍTKA ŠTUKOVÁ MJB MALBA JEDNOBAREVNÁ BÍLÁ PO PÓROVINOVÝ OBKLAD SDK SÁDROKARTONOVÝ PODHLED (7/T) TH PODHLED THERMATEX 600/600 mm (8/T)

POZNÁMKA :

STROPY V OBYTNÝCH I NEOBYTNÝCH MÍSTNOSTECH BYTOVÝCH JEDNOTEK MOHOU BÝT OPATŘENY SDK PODHLEDY na s.v. 2,54 m (DLE VYHL. 146/2024 SB. min s.v. = 2,50 m)

SEZNAM STAVEBNÍCH ÚPRAV :

ⓧ DECENTRÁLNÍ VĚTRACÍ REKUPERAČNÍ SYSTÉM se ZPĚTNÝM ZISKEM TEPLA (určený pro použití do prostorů s exponovaným venkovním hlukem) např. A-INVENT iV 14 – Zero, průměr otvoru 225 mm, tl. zdiva min. 255 mm, rozměr průchodky Ø 200 x 495/745 mm, průtok vzduchu v režimu zpětný zisk tepla 8,5–29 m3/h, hladina akustického tlaku (hlučnost) ve 2 m 10–31 dB(A) – 7 ks/patro

±0,000 = PODLAHA 1. NP = 183,960 m.n.m., výškový systém B.p.V.

ZMĚNA STAVBY PŘED DOKONČENÍM č. 1

VEDOUCÍ PROJEKTANT	VYPRACOVAL	OBJEKT SO-101 APARTMÁNOVÝ-bytový DŮM
ING. ARCH. RADKO PAVLACKÝ	ING. MICHAL NÁJEMNÍK	

PROJEKTOVÁ KANCELÁŘ
FABEDI s.r.o.
Nám.3. května 1605
765 02 Otrokovice
IČ: 116 78 852

INVESTOR: KŘETÍNSKÝ INVEST s.r.o., nám. 3. května 1820, 765 02 Otrokovice, IČO: 037 96 884

APARTMÁNOVÝ - BYTOVÝ DŮM V OTROKOVICÍCH
parc. č.st. 2120, 439/175, 439/117, 439/88, k.ú. Otrokovice

D.1.1 - ARCHITEKTONICKO - STAVEBNÍ ŘEŠENÍ

DATUM	09. 2026
FORMÁT	10 x A4
STUPEŇ	ZSD č. 1
ZAK. ČÍSLO	25 - 01
MĚŘÍTKO	1 : 50

PŮDORYS 2. NP | ZSD č. 1 | D 1.1 | 101/06