ZSD č. 1 – SO 101 – PŮDORYS 3. NP

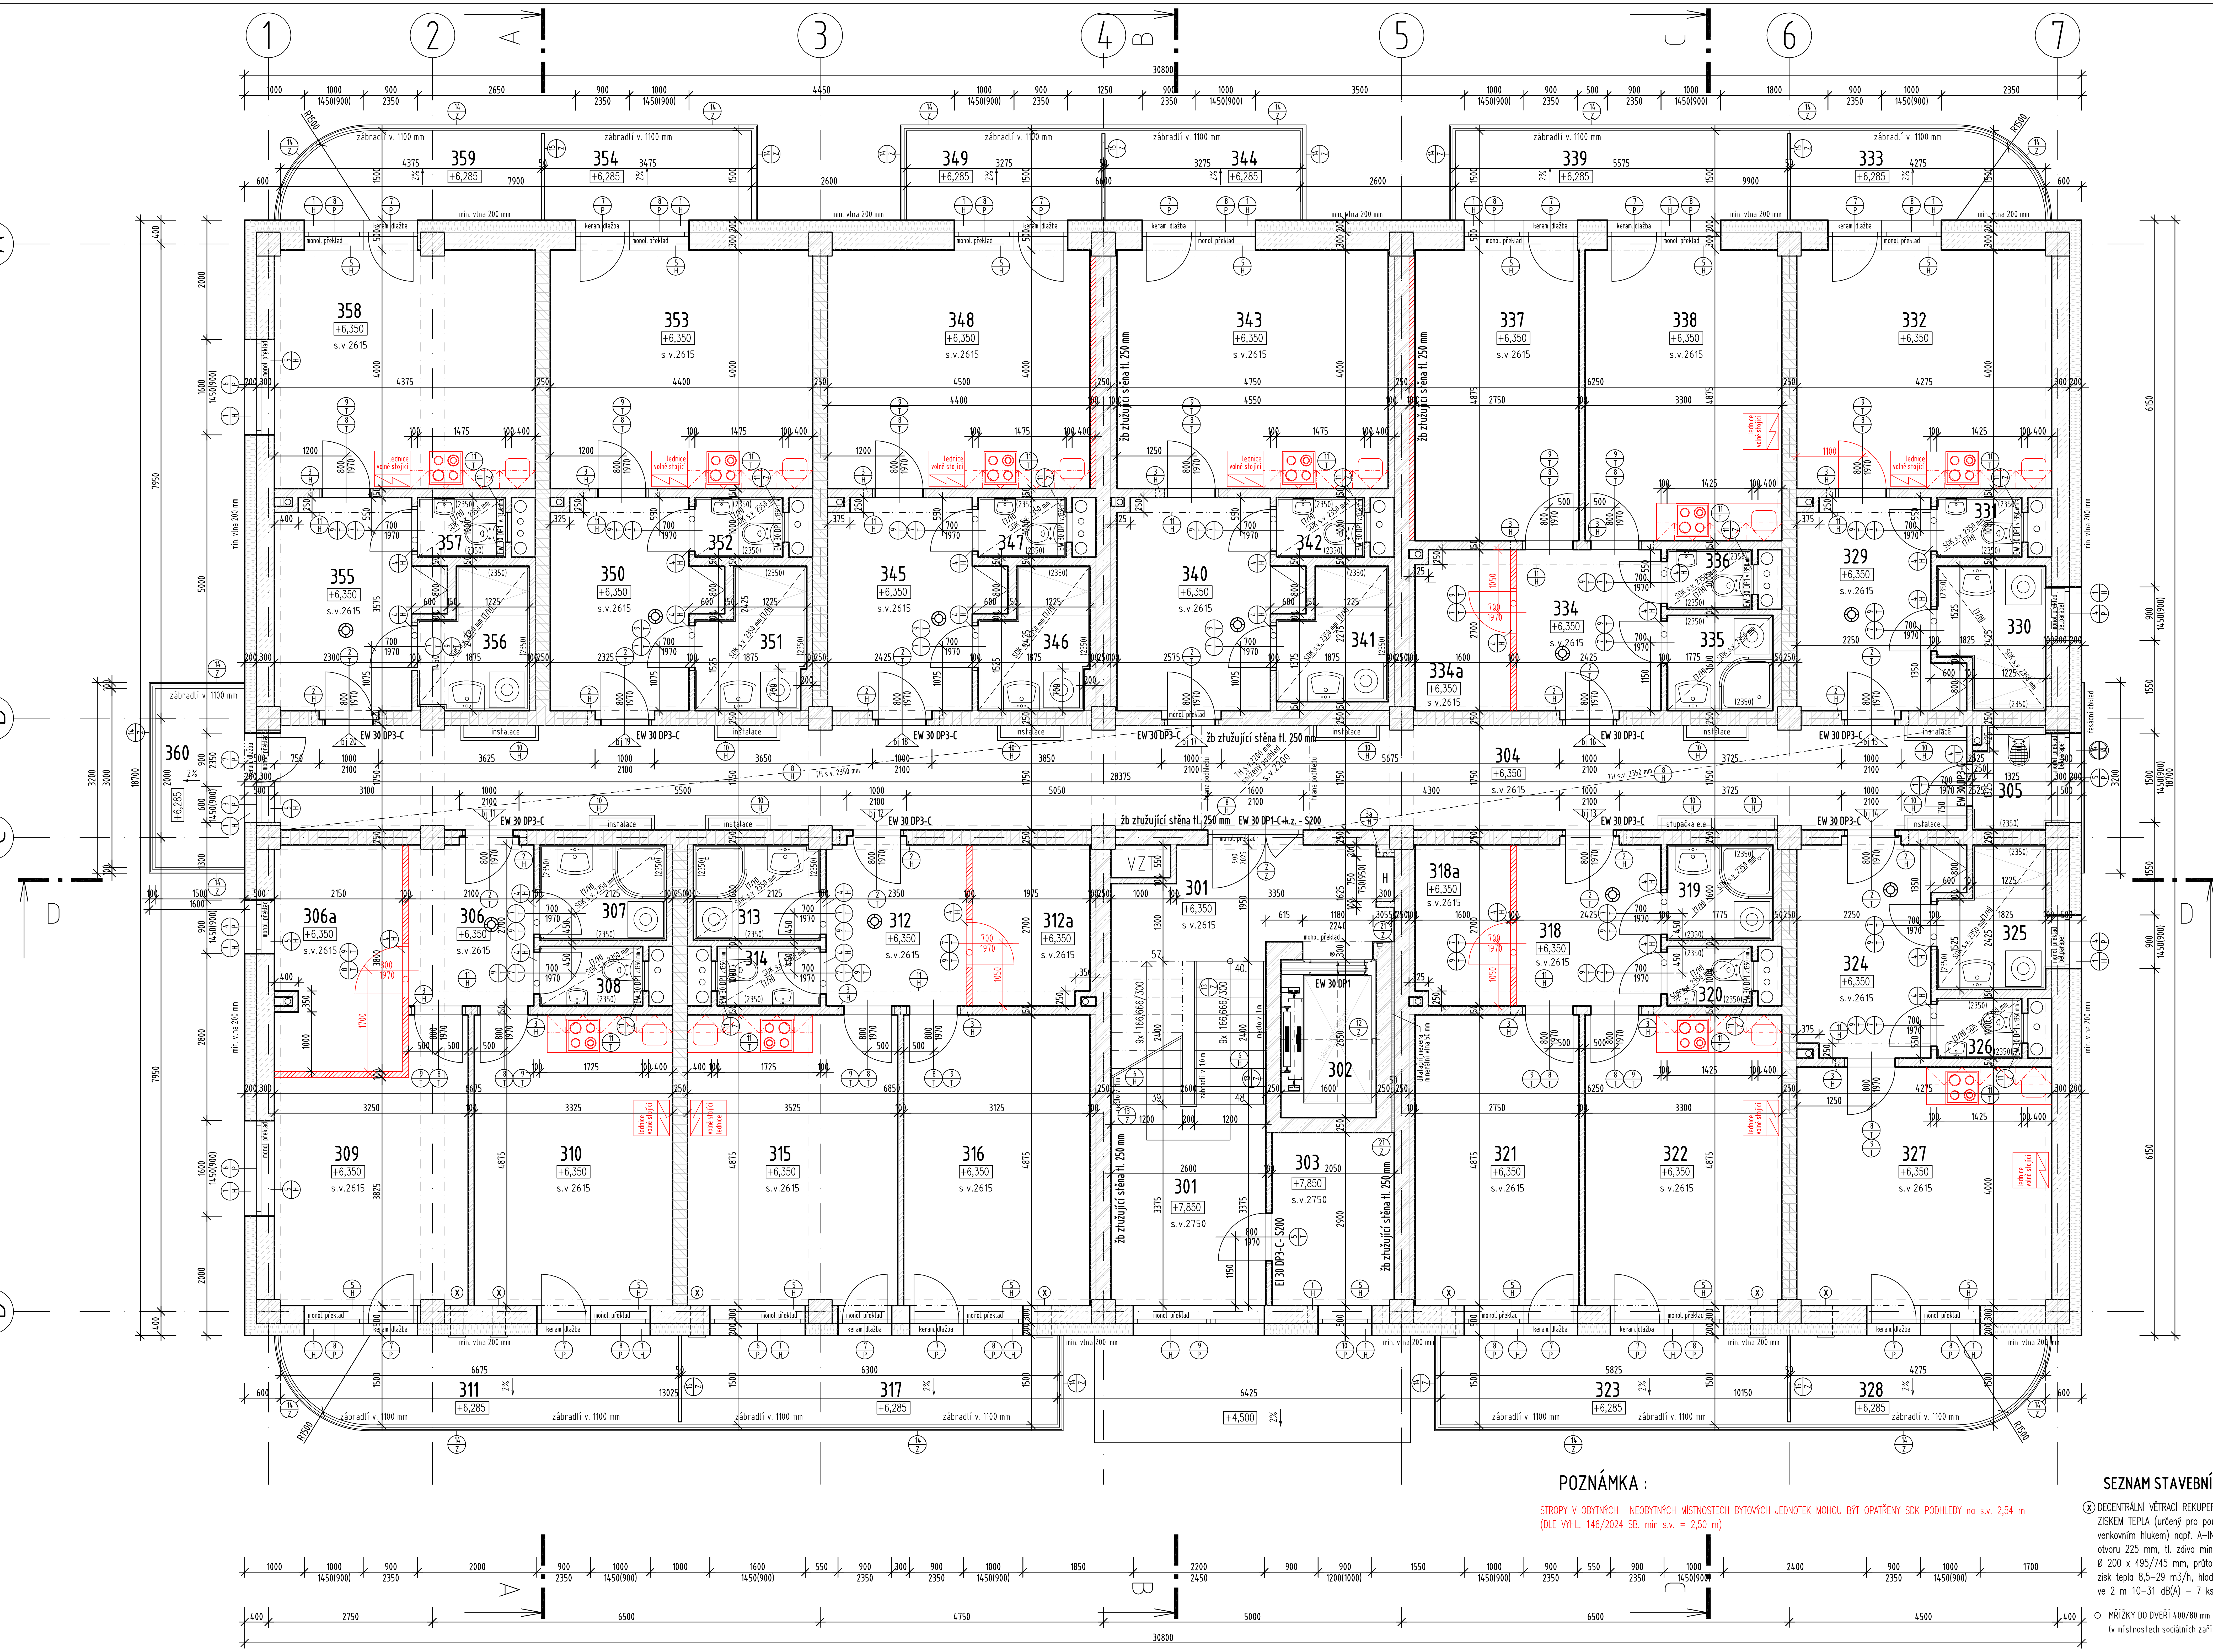

POZNÁMKA :

STROPY V OBYTNÝCH I NEOBYTNÝCH MÍSTNOSTECH BYTOVÝCH JEDNOTEK MOHOU BÝT OPATŘENY SDK PODHLEDY na s.v. 2,54 m (DLE VYHL. 146/2024 SB. min s.v. = 2,50 m)

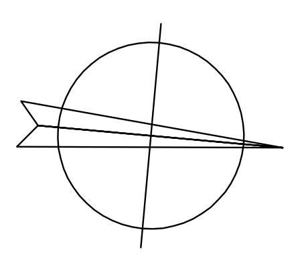

LEGENDA ZDIVA 3. NP

- ● ▨ ŽELEZOBETONOVÉ MONOLITICKÉ NOSNÉ KONSTRUKCE (sloupy ø500, 400/400 mm, pilíře, stropní desky, ztužující stěny, opěrné stěny, výtahová šachta) SOUČÁST STATICKÉ ČÁSTI DOKUMENTACE
- ▨ ODBODOVÉ VÝPLŇOVÉ ZDIVO Z BROUŠENÝCH BLOKŮ POROTHERM 30 PROFI (247x300x249 mm) tl. 300 mm PEVNOSTI P15 VYZDÍVANÉ NA MALTU PRO TENKÉ SPÁRY (na zdivu proveden kontaktní zateplovací systém s min. vlnou tl. 200 mm, ostění otvorů zatepleno min. vlnou tl. min. 30 mm)
- ◎ ZAŘÍZENÍ AUTONOMNÍ DETEKCE a SIGNALIZACE POŽÁRU (dle PBŘ stavby)
- ▨ MEZIBYTOVÉ STĚNY Z BLOKŮ Cihla Porotherm 25 AKU SYM – Akustická P 15 (rozměr 372 x 238 x 250 mm) tl. 250 mm, akustický cihelný blok s maltovou kapsou pro tl. stěny 25 cm na maltu M 10. Cihly jsou velmi vhodné pro mezibytové příčky tloušťky 250 mm. ZVUKOVÁ IZOLACE ZDIVA Rw = 57 dB (plošná hm. zdiva včetně omítek min. 313 kg/m2)
- ▨ ZDIVO PŘÍČEK Z PŘÍČKOVEK PORFIX TL. 100 mm a 150 mm VYZDÍVANÉ NA TMEL PORFIX (příčky, přizdívky), OMÍTKY VYZTUŽIT PERLINKOU

LEGENDA MÍSTNOSTÍ 3. NP

1 : 50

ČÍSLO	NÁZEV	PLOCHA[m2]	PODLAHA		STĚNY, STROP	POZNÁMKA
301	SCHODIŠTĚ	22,55	KERAMICKÁ DLAŽBA	D,E1	VOS, MJB	KERAMICKÉ STUPNĚ
302	VÝTAHOVÁ ŠACHTA	4,25	BETONOVÁ PODLAHA	x	VOS, MJB	
303	~~SKLAD PRÁDLA~~ KOMORA č. 32	5,95	KERAMICKÁ DLAŽBA	D	VOS, MJB	
304	CHODBA	49,30	KERAMICKÁ DLAŽBA	E1	VOS, MJB	TH s.v. 2200 mm TH s.v. 2350 mm
305	ÚKLIDOVÁ KOMORA	2,20	KERAMICKÁ DLAŽBA	E1	VOS, MJB, PO	PO v. 2100 mm
	BYTOVÁ JEDNOTKA č. 11	(plocha : 48,85 m2 + balkon 10,35 m2)				
306	PŘEDSÍŇ	5,65	VINYL tl. 3 mm (lepený)	G	VOS, MJB	
306a	KOMORA	8,05	VINYL tl. 3 mm (lepený)	G	VOS, MJB	
307	KOUPELNA	3,40	KERAMICKÁ DLAŽBA	F	VOS, MJB, PO, SDK	SDK s.v. 2350 mm PO v. 2350 mm
308	WC	1,75	KERAMICKÁ DLAŽBA	F	VOS, MJB, PO, SDK	SDK s.v. 2350 mm PO v. 2350 mm
309	POKOJ	13,40	VINYL tl. 3 mm (lepený)	G	VOS, MJB	
310	POKOJ + KK	16,60	VINYL tl. 3 mm (lepený)	G	VOS, MJB	
311	BALKON	10,35	DLAŽBA NA TERČÍCH	H	viz fasáda	
	BYTOVÁ JEDNOTKA č. 12	(plocha : 49,85 m2 + balkon 9,45 m2)				
312	PŘEDSÍŇ	6,35	VINYL tl. 3 mm (lepený)	G	VOS, MJB	
312a	KOMORA	5,25	VINYL tl. 3 mm (lepený)	G	VOS, MJB	
313	KOUPELNA	3,40	KERAMICKÁ DLAŽBA	F	VOS, MJB, PO, SDK	SDK s.v. 2350 mm PO v. 2350 mm
314	WC	1,75	KERAMICKÁ DLAŽBA	F	VOS, MJB, PO, SDK	SDK s.v. 2350 mm PO v. 2350 mm
315	POKOJ	17,50	VINYL tl. 3 mm (lepený)	G	VOS, MJB	
316	POKOJ	15,60	VINYL tl. 3 mm (lepený)	G	VOS, MJB	
317	BALKON	9,45	DLAŽBA NA TERČÍCH	H	viz fasáda	
	BYTOVÁ JEDNOTKA č. 13	(plocha : 44,95 m2 + balkon 8,75 m2)				
318	PŘEDSÍŇ	6,55	VINYL tl. 3 mm (lepený)	G	VOS, MJB	
318a	KOMORA	4,25	VINYL tl. 3 mm (lepený)	G	VOS, MJB	
319	KOUPELNA	2,80	KERAMICKÁ DLAŽBA	F	VOS, MJB, PO, SDK	SDK s.v. 2350 mm PO v. 2350 mm
320	WC	1,45	KERAMICKÁ DLAŽBA	F	VOS, MJB, PO, SDK	SDK s.v. 2350 mm PO v. 2350 mm
321	POKOJ	13,60	VINYL tl. 3 mm (lepený)	G	VOS, MJB	
322	POKOJ + KK	16,30	VINYL tl. 3 mm (lepený)	G	VOS, MJB	
323	BALKON	8,75	DLAŽBA NA TERČÍCH	H	viz fasáda	
	BYTOVÁ JEDNOTKA č. 14	(plocha : 31,25 m2 + balkon 6,75 m2)				
324	PŘEDSÍŇ	8,60	VINYL tl. 3 mm (lepený)	G	VOS, MJB	
325	KOUPELNA	3,90	KERAMICKÁ DLAŽBA	F	VOS, MJB, PO, SDK	SDK s.v. 2350 mm PO v. 2350 mm
326	WC	1,45	KERAMICKÁ DLAŽBA	F	VOS, MJB, PO, SDK	SDK s.v. 2350 mm PO v. 2350 mm
327	POKOJ + KK	17,30	VINYL tl. 3 mm (lepený)	G	VOS, MJB	
328	BALKON	6,75	DLAŽBA NA TERČÍCH	H	viz fasáda	
	BYTOVÁ JEDNOTKA č. 15	(plocha : 31,25 m2 + balkon 6,75 m2)				
329	PŘEDSÍŇ	8,60	VINYL tl. 3 mm (lepený)	G	VOS, MJB	
330	KOUPELNA	3,90	KERAMICKÁ DLAŽBA	F	VOS, MJB, PO, SDK	SDK s.v. 2350 mm PO v. 2350 mm
331	WC	1,45	KERAMICKÁ DLAŽBA	F	VOS, MJB, PO, SDK	SDK s.v. 2350 mm PO v. 2350 mm
332	POKOJ + KK	17,30	VINYL tl. 3 mm (lepený)	G	VOS, MJB	
333	BALKON	6,75	DLAŽBA NA TERČÍCH	H	viz fasáda	
	BYTOVÁ JEDNOTKA č. 16	(plocha : 44,95 m2 + balkon 8,35 m2)				
334	PŘEDSÍŇ	6,55	VINYL tl. 3 mm (lepený)	G	VOS, MJB	
334a	KOMORA	4,25	VINYL tl. 3 mm (lepený)	G	VOS, MJB	
335	KOUPELNA	2,80	KERAMICKÁ DLAŽBA	F	VOS, MJB, PO, SDK	SDK s.v. 2350 mm PO v. 2350 mm
336	WC	1,45	KERAMICKÁ DLAŽBA	F	VOS, MJB, PO, SDK	SDK s.v. 2350 mm PO v. 2350 mm
337	POKOJ	13,60	VINYL tl. 3 mm (lepený)	G	VOS, MJB	
338	POKOJ + KK	16,30	VINYL tl. 3 mm (lepený)	G	VOS, MJB	
339	BALKON	8,35	DLAŽBA NA TERČÍCH	H	viz fasáda	
	BYTOVÁ JEDNOTKA č. 17	(plocha : 32,90 m2 + balkon 4,90 m2)				
340	PŘEDSÍŇ	9,30	VINYL tl. 3 mm (lepený)	G	VOS, MJB	
341	KOUPELNA	3,70	KERAMICKÁ DLAŽBA	F	VOS, MJB, PO, SDK	SDK s.v. 2350 mm PO v. 2350 mm
342	WC	1,50	KERAMICKÁ DLAŽBA	F	VOS, MJB, PO, SDK	PO v. 2350 mm
343	POKOJ + KK	18,40	VINYL tl. 3 mm (lepený)	G	VOS, MJB	
344	BALKON	4,90	DLAŽBA NA TERČÍCH	H	viz fasáda	
	BYTOVÁ JEDNOTKA č. 18	(plocha : 31,85 m2 + balkon 4,90 m2)				
345	PŘEDSÍŇ	8,70	VINYL tl. 3 mm (lepený)	G	VOS, MJB	
346	KOUPELNA	3,85	KERAMICKÁ DLAŽBA	F	VOS, MJB, PO, SDK	SDK s.v. 2350 mm PO v. 2350 mm
347	WC	1,50	KERAMICKÁ DLAŽBA	F	VOS, MJB, PO, SDK	SDK s.v. 2350 mm PO v. 2350 mm
348	POKOJ + KK	17,80	VINYL tl. 3 mm (lepený)	G	VOS, MJB	
349	BALKON	4,90	DLAŽBA NA TERČÍCH	H	viz fasáda	
	BYTOVÁ JEDNOTKA č. 19	(plocha : 31,55 m2 + balkon 5,20 m2)				
350	PŘEDSÍŇ	8,40	VINYL tl. 3 mm (lepený)	G	VOS, MJB	
351	KOUPELNA	3,85	KERAMICKÁ DLAŽBA	F	VOS, MJB, PO, SDK	SDK s.v. 2350 mm PO v. 2350 mm
352	WC	1,50	KERAMICKÁ DLAŽBA	F	VOS, MJB, PO, SDK	SDK s.v. 2350 mm PO v. 2350 mm
353	POKOJ + KK	17,80	VINYL tl. 3 mm (lepený)	G	VOS, MJB	
354	BALKON	5,20	DLAŽBA NA TERČÍCH	H	viz fasáda	
	BYTOVÁ JEDNOTKA č. 20	(plocha : 31,80 m2 + balkon 6,90 m2)				
355	PŘEDSÍŇ	8,75	VINYL tl. 3 mm (lepený)	G	VOS, MJB	
356	KOUPELNA	3,90	KERAMICKÁ DLAŽBA	F	VOS, MJB, PO, SDK	SDK s.v. 2350 mm PO v. 2350 mm
357	WC	1,50	KERAMICKÁ DLAŽBA	F	VOS, MJB, PO, SDK	SDK s.v. 2350 mm PO v. 2350 mm
358	POKOJ + KK	17,65	VINYL tl. 3 mm (lepený)	G	VOS, MJB	
359	BALKON	6,90	DLAŽBA NA TERČÍCH	H	viz fasáda	
360	BALKON	4,50	DLAŽBA NA TERČÍCH	H	viz fasáda	

POZNÁMKA:
VOS VÁPENNÁ OMÍTKA ŠTUKOVÁ
MJB MALBA JEDNOBAREVNÁ BÍLÁ
PO PÓROVINOVÝ OBKLAD
SDK SÁDROKARTONOVÝ PODHLED (7/T)
TH PODHLED THERMATEX 600/600 mm (8/T)

SEZNAM STAVEBNÍCH ÚPRAV :

- (X) DECENTRÁLNÍ VĚTRACÍ REKUPERAČNÍ SYSTÉM se ZPĚTNÝM ZISKEM TEPLA (určený pro použití do prostorů s exponovaným venkovním hlukem) např. A–INVENT iV 14 – Zero, průměr otvoru 225 mm, tl. zdiva min. 255 mm, rozměr průchodky Ø 200 x 495/745 mm, průtok vzduchu v režimu zpětný zisk tepla 8,5–29 m3/h, hladina akustického tlaku (hlučnost) ve 2 m 10–31 dB(A) – 7 ks/patro
- ○ MŘÍŽKY DO DVEŘÍ 400/80 mm vřezané ke spodní hraně dveří (v místnostech sociálních zařízení s podtlakovým větráním) -12/T

±0,000 = PODLAHA 1. NP = 183,960 m.n.m., výškový systém B.p.V.

ZMĚNA STAVBY PŘED DOKONČENÍM č. 1

VEDOUCÍ PROJEKTANT	VYPRACOVAL	OBJEKT SO-101
ING. ARCH. RADKO PAVLACKÝ	ING. MICHAL NÁJEMNÍK	APARTMÁNOVÝ-bytový DŮM

PROJEKTOVÁ KANCELÁŘ
FABEDI s.r.o.
Nám.3. května 1605
765 02 Otrokovice
IČ: 116 78 852

INVESTOR: KŘETÍNSKÝ INVEST s.r.o., nám. 3. května 1820, 765 02 Otrokovice, IČO: 037 96 884

APARTMÁNOVÝ – BYTOVÝ DŮM V OTROKOVICÍCH
parc. č.st. 2120, 439/175, 439/117, 439/88, k.ú. Otrokovice

D.1.1 – ARCHITEKTONICKO – STAVEBNÍ ŘEŠENÍ

DATUM	09. 2026
FORMÁT	10 x A4
STUPEŇ	ZSD č. 1
ZAK. ČÍSLO	25 – 01
MĚŘÍTKO	1 : 50

PŮDORYS 3. NP — ZSD č. 1 — D 1.1 — 101/07