ZSD č. 1 – SO 101 – PŮDORYS 4. NP

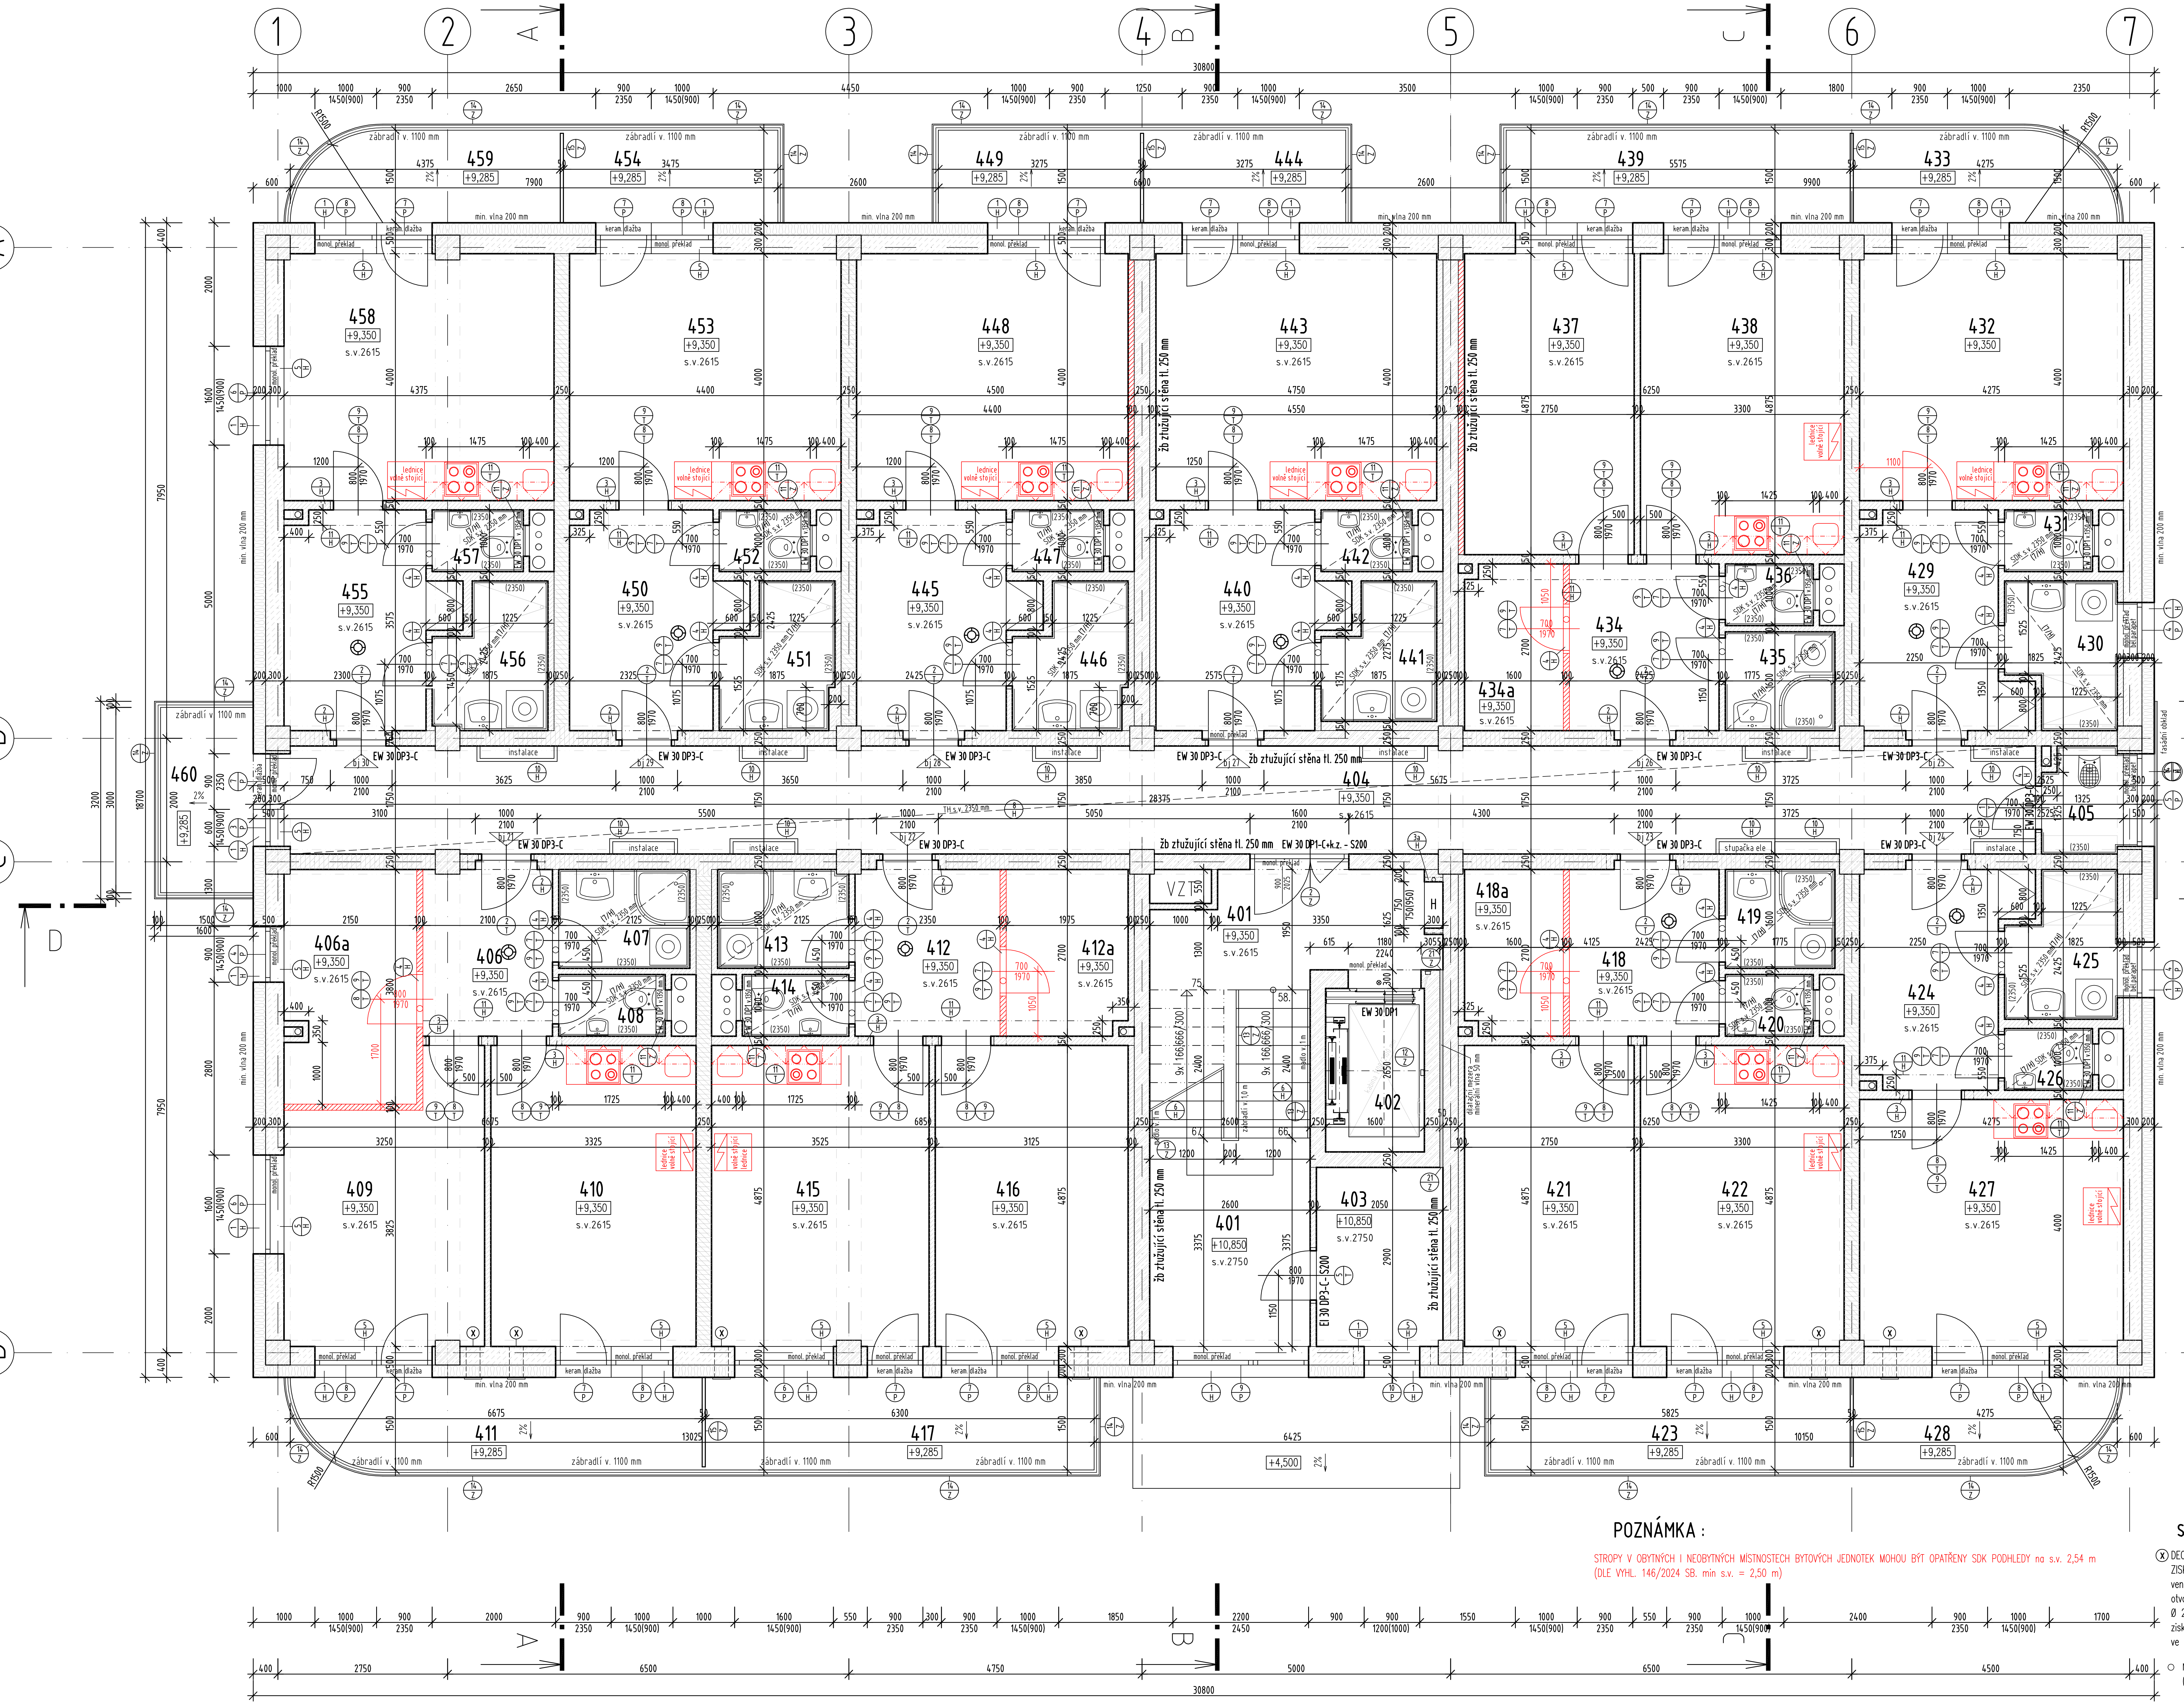

POZNÁMKA :

STROPY V OBYTNÝCH I NEOBYTNÝCH MÍSTNOSTECH BYTOVÝCH JEDNOTEK MOHOU BÝT OPATŘENY SDK PODHLEDY na s.v. 2,54 m (DLE VYHL. 146/2024 SB. min s.v. = 2,50 m)

SEZNAM STAVEBNÍCH ÚPRAV :

ⓧ DECENTRÁLNÍ VĚTRACÍ REKUPERAČNÍ SYSTÉM se ZPĚTNÝM ZISKEM TEPLA (určený pro použití do prostorů s exponovaným venkovním hlukem) např. A–INVENT iV 14 – Zero, průměr otvoru 225 mm, tl. zdiva min. 255 mm, rozměr průchodky Ø 200 x 495/745 mm, průtok vzduchu v režimu zpětný zisk tepla 8,5–29 m3/h, hladina akustického tlaku (hlučnost) ve 2 m 10–31 dB(A) – 7 ks/patro

○ MŘÍŽKY DO DVEŘÍ 400/80 mm vřezané ke spodní hraně dveří (v místnostech sociálních zařízení s podtlakovým větráním) -12/T

LEGENDA ZDIVA 4. NP

▨ ŽELEZOBETONOVÉ MONOLITICKÉ NOSNÉ KONSTRUKCE (sloupy Ø500, 400/400 mm, pilíře, stropní desky, ztužující stěny, opěrné stěny, výtahová šachta) SOUČÁST STATICKÉ ČÁSTI DOKUMENTACE

▨ ODBODOVÉ VÝPLŇOVÉ ZDIVO Z BROUŠENÝCH BLOKŮ POROTHERM 30 PROFI (247x300x249 mm) tl. 300 mm PEVNOSTI P15 VYZDÍVANÉ NA MALTU PRO TENKÉ SPÁRY (na zdivu proveden kontaktní zateplovací systém s min. vlnou tl. 200 mm, ostění otvorů zatepleno min. vlnou tl. min. 30 mm)

◎ ZAŘÍZENÍ AUTONOMNÍ DETEKCE a SIGNALIZACE POŽÁRU (dle PBŘ stavby)

▨ MEZIBYTOVÉ STĚNY Z BLOKŮ Cihla Porotherm 25 AKU SYM – Akustická P 15 (rozměr 372 x 238 x 250 mm) tl. 250 mm, akustický cihelný blok s maltovou kapsou pro tl. stěny 25 cm na maltu M 10. Cihly jsou velmi vhodné pro mezibytové příčky tloušťky 250 mm. ZVUKOVÁ IZOLACE ZDIVA Rw = 57 dB (plošná hm. zdiva včetně omítek min. 313 kg/m2)

▨ ZDIVO PŘÍČEK Z PŘÍČKOVEK PORFIX TL. 100 mm a 150 mm VYZDÍVANÉ NA TMEL PORFIX (příčky, přizdívky), OMÍTKY VYZTUŽIT PERLINKOU

LEGENDA MÍSTNOSTÍ 4. NP

1 : 50

ČÍSLO	NÁZEV	PLOCHA[m2]	PODLAHA		STĚNY, STROP	POZNÁMKA
401	SCHODIŠTĚ	22,55	KERAMICKÁ DLAŽBA	D,E1	VOS, MJB	KERAMICKÉ STUPNĚ
402	VÝTAHOVÁ ŠACHTA	4,25	BETONOVÁ PODLAHA	x	VOS, MJB	
403	SKLAD PRÁDLA KOMORA č. 33	5,95	KERAMICKÁ DLAŽBA	D	VOS, MJB	
404	CHODBA	49,30	KERAMICKÁ DLAŽBA	E1	VOS, MJB	TH s.v. 2350 mm
405	ÚKLIDOVÁ KOMORA	2,20	KERAMICKÁ DLAŽBA	E1	VOS, MJB, PO	PO v. 2100 mm
BYTOVÁ JEDNOTKA č. 21 (plocha : 48,85 m2 + balkon 10,35 m2)						
406	PŘEDSÍŇ	5,65	VINYL tl. 3 mm (lepený)	G	VOS, MJB	
406a	KOMORA	8,05	VINYL tl. 3 mm (lepený)	G	VOS, MJB	
407	KOUPELNA	3,40	KERAMICKÁ DLAŽBA	F	VOS, MJB, PO, SDK	SDK s.v. 2350 mm PO v. 2350 mm
408	WC	1,75	KERAMICKÁ DLAŽBA	F	VOS, MJB, PO, SDK	SDK s.v. 2350 mm PO v. 2350 mm
409	POKOJ	13,40	VINYL tl. 3 mm (lepený)	G	VOS, MJB	
410	POKOJ + KK	16,60	VINYL tl. 3 mm (lepený)	G	VOS, MJB	
411	BALKON	10,35	DLAŽBA NA TERČÍCH	H	viz fasáda	
BYTOVÁ JEDNOTKA č. 22 (plocha : 49,85 m2 + balkon 9,45 m2)						
412	PŘEDSÍŇ	6,35	VINYL tl. 3 mm (lepený)	G	VOS, MJB	
412a	KOMORA	5,25	VINYL tl. 3 mm (lepený)	G	VOS, MJB	
413	KOUPELNA	3,40	KERAMICKÁ DLAŽBA	F	VOS, MJB, PO, SDK	SDK s.v. 2350 mm PO v. 2350 mm
414	WC	1,75	KERAMICKÁ DLAŽBA	F	VOS, MJB, PO, SDK	SDK s.v. 2350 mm PO v. 2350 mm
415	POKOJ + KK	17,50	VINYL tl. 3 mm (lepený)	G	VOS, MJB	
416	POKOJ	15,60	VINYL tl. 3 mm (lepený)	G	VOS, MJB	
417	BALKON	9,45	DLAŽBA NA TERČÍCH	H	viz fasáda	
BYTOVÁ JEDNOTKA č. 23 (plocha : 44,95 m2 + balkon 8,75 m2)						
418	PŘEDSÍŇ	6,55	VINYL tl. 3 mm (lepený)	G	VOS, MJB	
418a	KOMORA	4,25	VINYL tl. 3 mm (lepený)	G	VOS, MJB	
419	KOUPELNA	2,80	KERAMICKÁ DLAŽBA	F	VOS, MJB, PO, SDK	SDK s.v. 2350 mm PO v. 2350 mm
420	WC	1,45	KERAMICKÁ DLAŽBA	F	VOS, MJB, PO, SDK	SDK s.v. 2350 mm PO v. 2350 mm
421	POKOJ	13,60	VINYL tl. 3 mm (lepený)	G	VOS, MJB	
422	POKOJ + KK	16,30	VINYL tl. 3 mm (lepený)	G	VOS, MJB	
423	BALKON	8,75	DLAŽBA NA TERČÍCH	H	viz fasáda	
BYTOVÁ JEDNOTKA č. 24 (plocha : 31,25 m2 + balkon 6,75 m2)						
424	PŘEDSÍŇ, KUCHYNĚ	8,60	VINYL tl. 3 mm (lepený)	G	VOS, MJB	
425	KOUPELNA	3,90	KERAMICKÁ DLAŽBA	F	VOS, MJB, PO, SDK	SDK s.v. 2350 mm PO v. 2350 mm
426	WC	1,45	KERAMICKÁ DLAŽBA	F	VOS, MJB, PO, SDK	SDK s.v. 2350 mm PO v. 2350 mm
427	POKOJ + KK	17,30	VINYL tl. 3 mm (lepený)	G	VOS, MJB	
428	BALKON	6,75	DLAŽBA NA TERČÍCH	H	viz fasáda	
BYTOVÁ JEDNOTKA č. 25 (plocha : 31,25 m2 + balkon 6,75 m2)						
429	PŘEDSÍŇ, KUCHYNĚ	8,60	VINYL tl. 3 mm (lepený)	G	VOS, MJB	
430	KOUPELNA	3,90	KERAMICKÁ DLAŽBA	F	VOS, MJB, PO, SDK	SDK s.v. 2350 mm PO v. 2350 mm
431	WC	1,45	KERAMICKÁ DLAŽBA	F	VOS, MJB, PO, SDK	SDK s.v. 2350 mm PO v. 2350 mm
432	POKOJ + KK	17,30	VINYL tl. 3 mm (lepený)	G	VOS, MJB	
433	BALKON	6,75	DLAŽBA NA TERČÍCH	H	viz fasáda	
BYTOVÁ JEDNOTKA č. 26 (plocha : 44,95 m2 + balkon 8,35 m2)						
434	PŘEDSÍŇ	6,55	VINYL tl. 3 mm (lepený)	G	VOS, MJB	
434a	KOMORA	4,25	VINYL tl. 3 mm (lepený)	G	VOS, MJB	
435	KOUPELNA	2,80	KERAMICKÁ DLAŽBA	F	VOS, MJB, PO, SDK	SDK s.v. 2350 mm PO v. 2350 mm
436	WC	1,45	KERAMICKÁ DLAŽBA	F	VOS, MJB, PO, SDK	SDK s.v. 2350 mm PO v. 2350 mm
437	POKOJ	13,60	VINYL tl. 3 mm (lepený)	G	VOS, MJB	
438	POKOJ + KK	16,30	VINYL tl. 3 mm (lepený)	G	VOS, MJB	
439	BALKON	8,35	DLAŽBA NA TERČÍCH	H	viz fasáda	
BYTOVÁ JEDNOTKA č. 27 (plocha : 32,90 m2 + balkon 4,90 m2)						
440	PŘEDSÍŇ, KUCHYNĚ	9,30	VINYL tl. 3 mm (lepený)	G	VOS, MJB	
441	KOUPELNA	3,70	KERAMICKÁ DLAŽBA	F	VOS, MJB, PO, SDK	SDK s.v. 2350 mm PO v. 2350 mm
442	WC	1,50	KERAMICKÁ DLAŽBA	F	VOS, MJB, PO, SDK	PO v. 2350 mm
443	POKOJ + KK	18,40	VINYL tl. 3 mm (lepený)	G	VOS, MJB	
444	BALKON	4,90	DLAŽBA NA TERČÍCH	H	viz fasáda	
BYTOVÁ JEDNOTKA č. 28 (plocha : 32,25 m2 + balkon 4,90 m2)						
445	PŘEDSÍŇ, KUCHYNĚ	8,70	VINYL tl. 3 mm (lepený)	G	VOS, MJB	
446	KOUPELNA	3,80	KERAMICKÁ DLAŽBA	F	VOS, MJB, PO, SDK	SDK s.v. 2350 mm PO v. 2350 mm
447	WC	1,50	KERAMICKÁ DLAŽBA	F	VOS, MJB, PO, SDK	SDK s.v. 2350 mm PO v. 2350 mm
448	POKOJ + KK	18,20	VINYL tl. 3 mm (lepený)	G	VOS, MJB	
449	BALKON	4,90	DLAŽBA NA TERČÍCH	H	viz fasáda	
BYTOVÁ JEDNOTKA č. 29 (plocha : 31,55 m2 + balkon 5,20 m2)						
450	PŘEDSÍŇ, KUCHYNĚ	8,40	VINYL tl. 3 mm (lepený)	G	VOS, MJB	
451	KOUPELNA	3,85	KERAMICKÁ DLAŽBA	F	VOS, MJB, PO, SDK	SDK s.v. 2350 mm PO v. 2350 mm
452	WC	1,50	KERAMICKÁ DLAŽBA	F	VOS, MJB, PO, SDK	SDK s.v. 2350 mm PO v. 2350 mm
453	POKOJ + KK	17,80	VINYL tl. 3 mm (lepený)	G	VOS, MJB	
454	BALKON	5,20	DLAŽBA NA TERČÍCH	H	viz fasáda	
BYTOVÁ JEDNOTKA č. 30 (plocha : 31,80 m2 + balkon 6,90 m2)						
455	PŘEDSÍŇ, KUCHYNĚ	8,75	VINYL tl. 3 mm (lepený)	G	VOS, MJB	
456	KOUPELNA	3,90	KERAMICKÁ DLAŽBA	F	VOS, MJB, PO, SDK	SDK s.v. 2350 mm PO v. 2350 mm
457	WC	1,50	KERAMICKÁ DLAŽBA	F	VOS, MJB, PO, SDK	SDK s.v. 2350 mm PO v. 2350 mm
458	POKOJ + KK	17,65	VINYL tl. 3 mm (lepený)	G	VOS, MJB	
459	BALKON	6,90	DLAŽBA NA TERČÍCH	H	viz fasáda	
460	BALKON	4,50	DLAŽBA NA TERČÍCH	H	viz fasáda	

POZNÁMKA: VOS VÁPENNÁ OMÍTKA ŠTUKOVÁ MJB MALBA JEDNOBAREVNÁ BÍLÁ PO PÓROVINOVÝ OBKLAD SDK SÁDROKARTONOVÝ PODHLED (7/T) TH PODHLED THERMATEX 600/600 mm (8/T)

±0,000 = PODLAHA 1. NP = 183,960 m.n.m., výškový systém B.p.V.

ZMĚNA STAVBY PŘED DOKONČENÍM č. 1

VEDOUCÍ PROJEKTANT ING. ARCH. RADKO PAVLACKÝ	VYPRACOVAL ING. MICHAL NÁJEMNÍK	OBJEKT SO-101 APARTMÁNOVÝ-bytový DŮM	PROJEKTOVÁ KANCELÁŘ FABEDI s.r.o. Nám.3. května 1605 765 02 Otrokovice IČ: 116 78 852

INVESTOR: KŘETÍNSKÝ INVEST s.r.o., nám. 3. května 1820, 765 02 Otrokovice, IČO: 037 96 884

APARTMÁNOVÝ - BYTOVÝ DŮM V OTROKOVICÍCH
parc. č.st. 2120, 439/175, 439/117, 439/88, k.ú. Otrokovice

D.1.1 - ARCHITEKTONICKO - STAVEBNÍ ŘEŠENÍ

DATUM	09. 2026
FORMÁT	10 x A4
STUPEŇ	ZSD č. 1
ZAK. ČÍSLO	25 - 01
MĚŘÍTKO	1 : 50

PŮDORYS 4. NP ZSD č. 1 D 1.1 101/08