ZSD č. 1 – SO 101 – PŮDORYS 6. NP

1 : 50

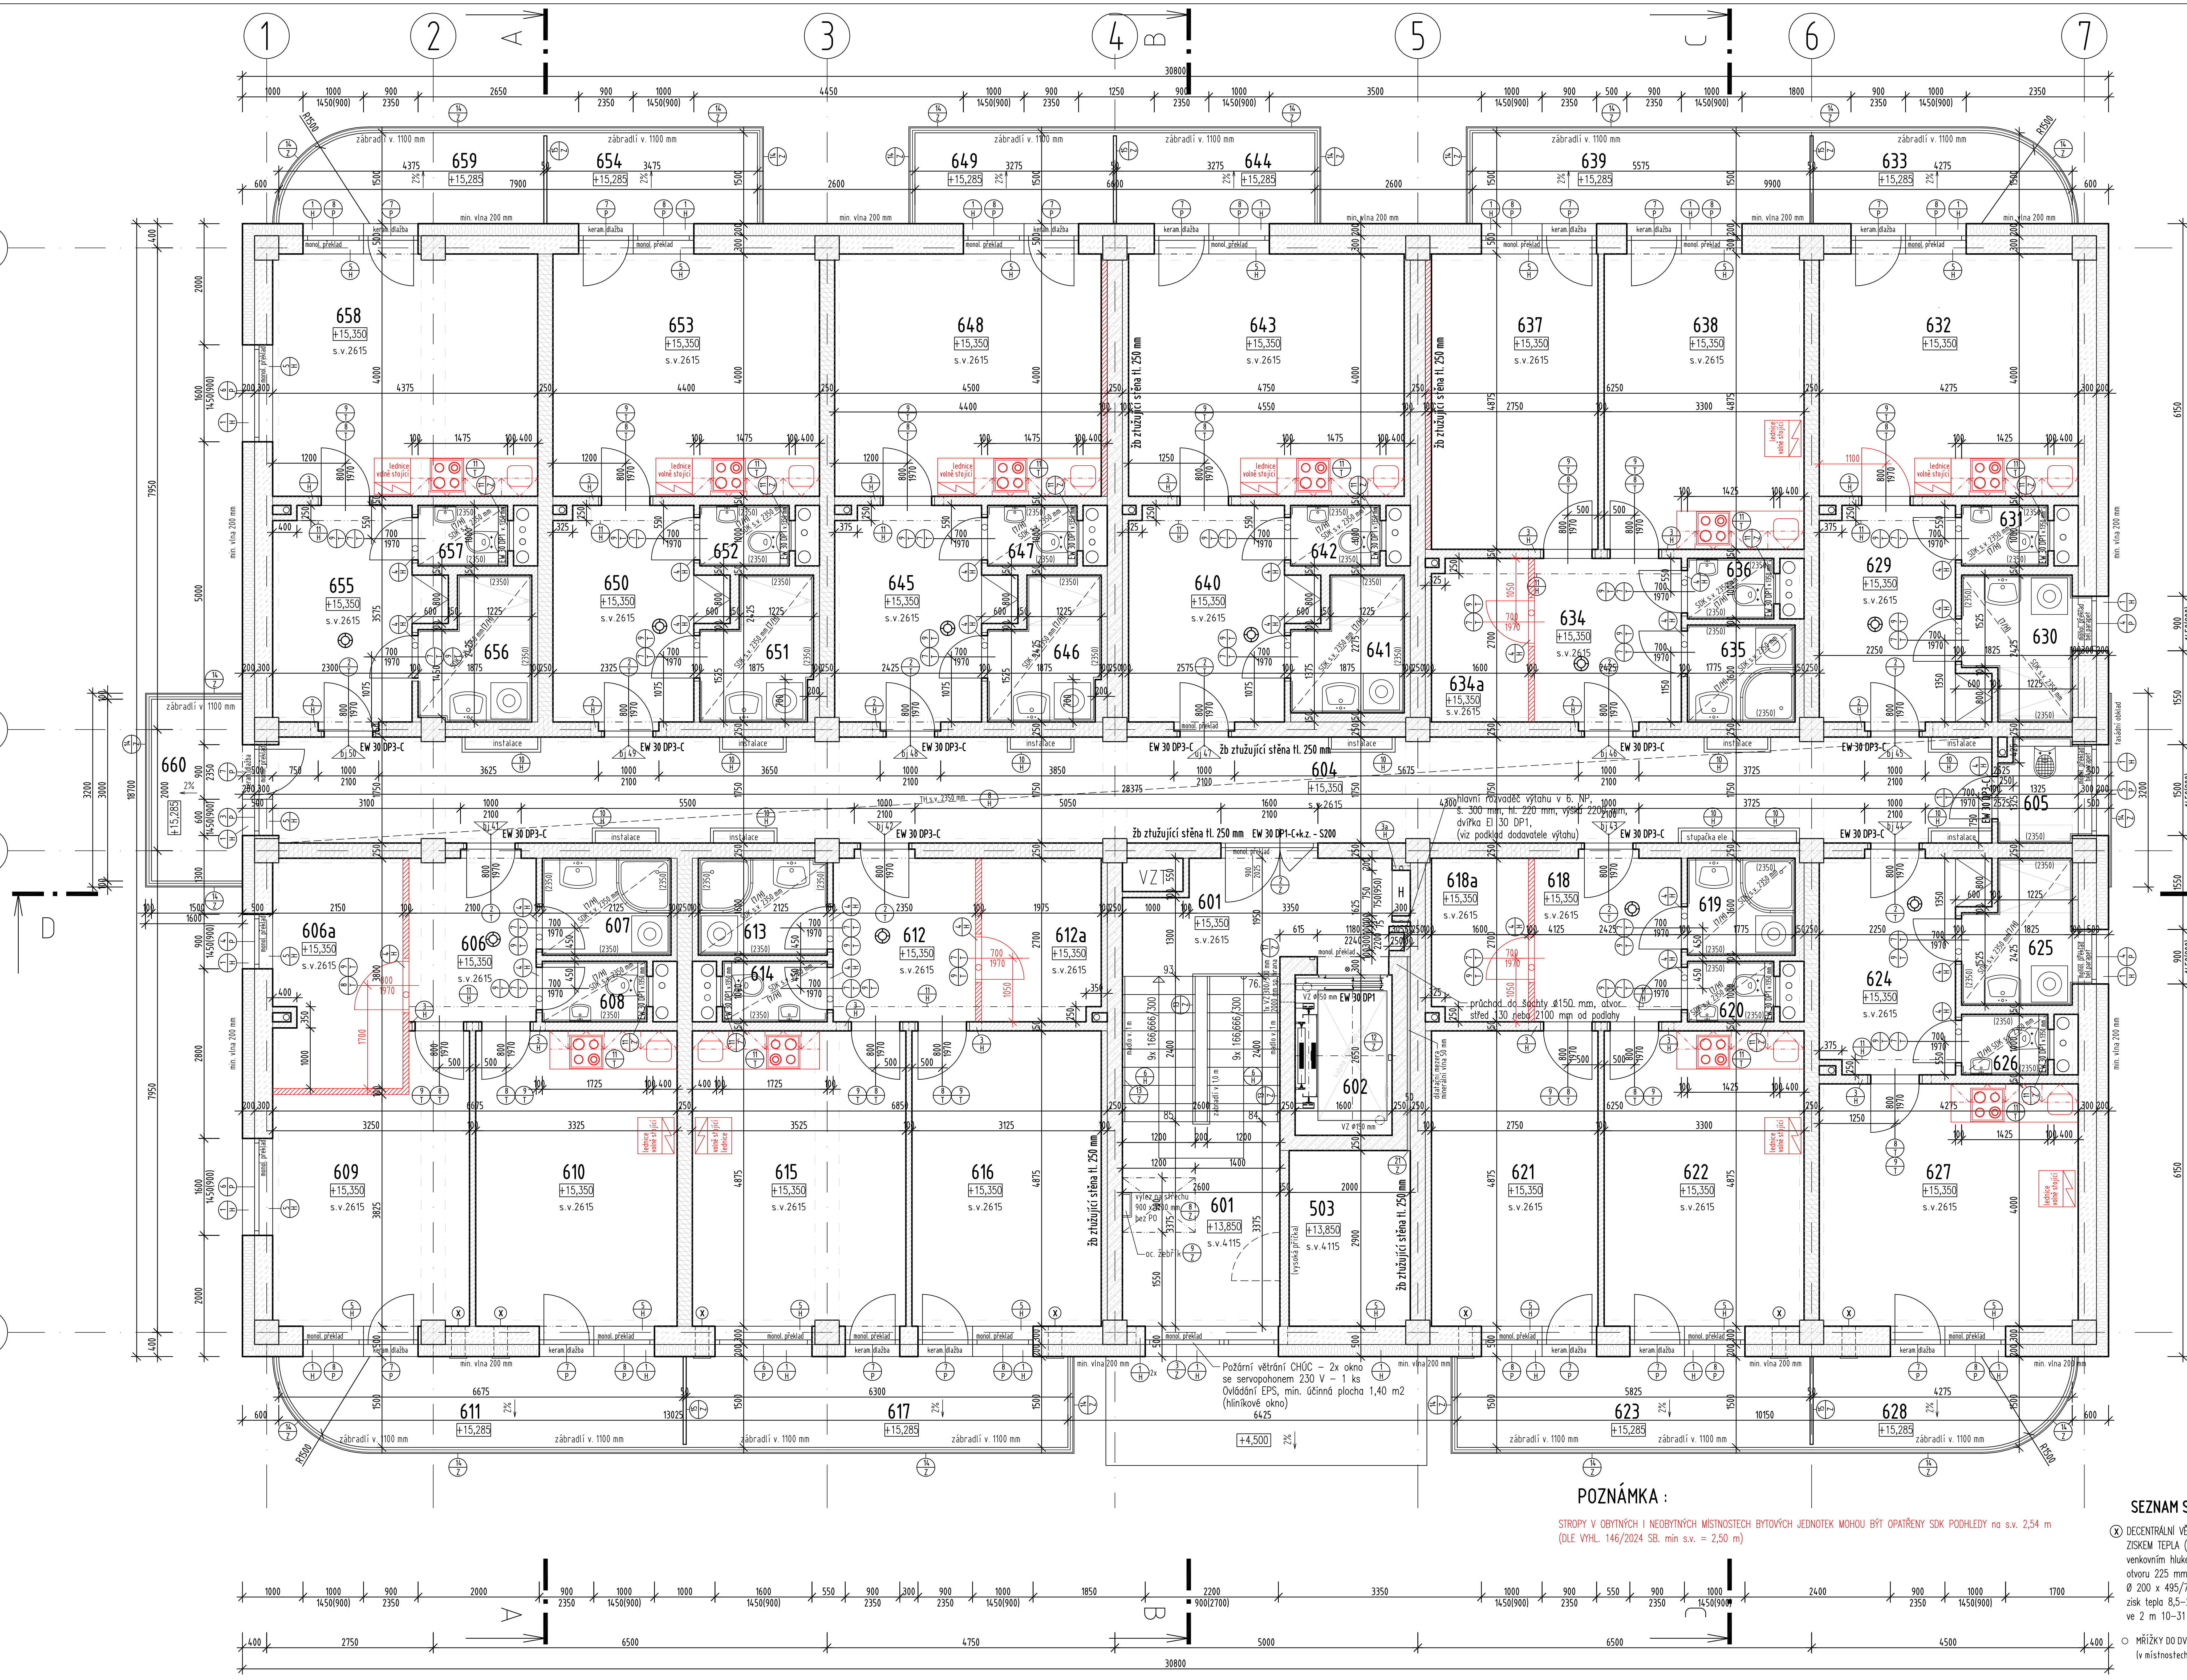

LEGENDA MÍSTNOSTÍ 6. NP

ČÍSLO	NÁZEV	PLOCHA[m2]	PODLAHA		STĚNY, STROP	POZNÁMKA
601	SCHODIŠTĚ	22,55	KERAMICKÁ DLAŽBA	D,E1	VOS, MJB	KERAMICKÉ STUPNĚ
602	VÝTAHOVÁ ŠACHTA	4,25	BETONOVÁ PODLAHA	x	VOS, MJB	
603	SKLAD PRÁDLA	5,80	KERAMICKÁ DLAŽBA	D	VOS, MJB	
604	CHODBA	49,30	KERAMICKÁ DLAŽBA	E1	VOS, MJB	TH s.v. 2350 mm
605	ÚKLIDOVÁ KOMORA	2,20	KERAMICKÁ DLAŽBA	E1	VOS, MJB, PO	PO v. 2100 mm
	BYTOVÁ JEDNOTKA č. 41	(plocha : 48,85 m2 + balkon 10,35 m2)				
606	PŘEDSÍŇ	5,65	VINYL tl. 3 mm (lepený)	G	VOS, MJB	
606a	KOMORA	8,05	VINYL tl. 3 mm (lepený)	G	VOS, MJB	
607	KOUPELNA	3,40	KERAMICKÁ DLAŽBA	F	VOS, MJB, PO, SDK	SDK s.v. 2350 mm PO v. 2350 mm
608	WC	1,75	KERAMICKÁ DLAŽBA	F	VOS, MJB, PO, SDK	SDK s.v. 2350 mm PO v. 2350 mm
609	POKOJ	13,40	VINYL tl. 3 mm (lepený)	G	VOS, MJB	
610	POKOJ + KK	16,60	VINYL tl. 3 mm (lepený)	G	VOS, MJB	
611	BALKON	10,35	DLAŽBA NA TERČÍCH	H	viz fasáda	
	BYTOVÁ JEDNOTKA č. 42	(plocha : 49,85 m2 + balkon 9,45 m2)				
612	PŘEDSÍŇ	6,35	VINYL tl. 3 mm (lepený)	G	VOS, MJB	
612a	KOMORA	5,25	VINYL tl. 3 mm (lepený)	G	VOS, MJB	
613	KOUPELNA	3,40	KERAMICKÁ DLAŽBA	F	VOS, MJB, PO, SDK	SDK s.v. 2350 mm PO v. 2350 mm
614	WC	1,75	KERAMICKÁ DLAŽBA	F	VOS, MJB, PO, SDK	SDK s.v. 2350 mm PO v. 2350 mm
615	POKOJ + KK	17,50	VINYL tl. 3 mm (lepený)	G	VOS, MJB	
616	POKOJ	15,60	VINYL tl. 3 mm (lepený)	G	VOS, MJB	
617	BALKON	9,45	DLAŽBA NA TERČÍCH	H	viz fasáda	
	BYTOVÁ JEDNOTKA č. 43	(plocha : 44,95 m2 + balkon 8,75 m2)				
618	PŘEDSÍŇ	6,55	VINYL tl. 3 mm (lepený)	G	VOS, MJB	
618a	KOMORA	4,25	VINYL tl. 3 mm (lepený)	G	VOS, MJB	
619	KOUPELNA	2,80	KERAMICKÁ DLAŽBA	F	VOS, MJB, PO, SDK	SDK s.v. 2350 mm PO v. 2350 mm
620	WC	1,45	KERAMICKÁ DLAŽBA	F	VOS, MJB, PO, SDK	SDK s.v. 2350 mm PO v. 2350 mm
621	POKOJ	13,60	VINYL tl. 3 mm (lepený)	G	VOS, MJB	
622	POKOJ + KK	16,30	VINYL tl. 3 mm (lepený)	G	VOS, MJB	
623	BALKON	8,75	DLAŽBA NA TERČÍCH	H	viz fasáda	
	BYTOVÁ JEDNOTKA č. 44	(plocha : 31,25 m2 + balkon 6,75 m2)				
624	PŘEDSÍŇ, KUCHYNĚ	8,60	VINYL tl. 3 mm (lepený)	G	VOS, MJB	
625	KOUPELNA	3,90	KERAMICKÁ DLAŽBA	F	VOS, MJB, PO, SDK	SDK s.v. 2350 mm PO v. 2350 mm
626	WC	1,45	KERAMICKÁ DLAŽBA	F	VOS, MJB, PO, SDK	SDK s.v. 2350 mm PO v. 2350 mm
627	POKOJ + KK	17,30	VINYL tl. 3 mm (lepený)	G	VOS, MJB	
628	BALKON	6,75	DLAŽBA NA TERČÍCH	H	viz fasáda	
	BYTOVÁ JEDNOTKA č. 45	(plocha : 31,25 m2 + balkon 6,75 m2)				
629	PŘEDSÍŇ, KUCHYNĚ	8,60	VINYL tl. 3 mm (lepený)	G	VOS, MJB	
630	KOUPELNA	3,90	KERAMICKÁ DLAŽBA	F	VOS, MJB, PO, SDK	SDK s.v. 2350 mm PO v. 2350 mm
631	WC	1,45	KERAMICKÁ DLAŽBA	F	VOS, MJB, PO, SDK	SDK s.v. 2350 mm PO v. 2350 mm
632	POKOJ + KK	17,30	VINYL tl. 3 mm (lepený)	G	VOS, MJB	
633	BALKON	6,75	DLAŽBA NA TERČÍCH	H	viz fasáda	
	BYTOVÁ JEDNOTKA č. 46	(plocha : 44,95 m2 + balkon 8,35 m2)				
634	PŘEDSÍŇ	6,55	VINYL tl. 3 mm (lepený)	G	VOS, MJB	
634a	KOMORA	4,25	VINYL tl. 3 mm (lepený)	G	VOS, MJB	
635	KOUPELNA	2,80	KERAMICKÁ DLAŽBA	F	VOS, MJB, PO, SDK	SDK s.v. 2350 mm PO v. 2350 mm
636	WC	1,45	KERAMICKÁ DLAŽBA	F	VOS, MJB, PO, SDK	SDK s.v. 2350 mm PO v. 2350 mm
637	POKOJ	13,60	VINYL tl. 3 mm (lepený)	G	VOS, MJB	
638	POKOJ + KK	16,30	VINYL tl. 3 mm (lepený)	G	VOS, MJB	
639	BALKON	8,35	DLAŽBA NA TERČÍCH	H	viz fasáda	
	BYTOVÁ JEDNOTKA č. 47	(plocha : 32,90 m2 + balkon 4,90 m2)				
640	PŘEDSÍŇ, KUCHYNĚ	9,30	VINYL tl. 3 mm (lepený)	G	VOS, MJB	
641	KOUPELNA	3,70	KERAMICKÁ DLAŽBA	F	VOS, MJB, PO, SDK	SDK s.v. 2350 mm PO v. 2350 mm
642	WC	1,50	KERAMICKÁ DLAŽBA	F	VOS, MJB, PO, SDK	PO v. 2350 mm
643	POKOJ + KK	18,40	VINYL tl. 3 mm (lepený)	G	VOS, MJB	
644	BALKON	4,90	DLAŽBA NA TERČÍCH	H	viz fasáda	
	BYTOVÁ JEDNOTKA č. 48	(plocha : 32,25 m2 + balkon 4,90 m2)				
645	PŘEDSÍŇ, KUCHYNĚ	8,70	VINYL tl. 3 mm (lepený)	G	VOS, MJB	
646	KOUPELNA	3,85	KERAMICKÁ DLAŽBA	F	VOS, MJB, PO, SDK	SDK s.v. 2350 mm PO v. 2350 mm
647	WC	1,50	KERAMICKÁ DLAŽBA	F	VOS, MJB, PO, SDK	SDK s.v. 2350 mm PO v. 2350 mm
648	POKOJ + KK	18,20	VINYL tl. 3 mm (lepený)	G	VOS, MJB	
649	BALKON	4,90	DLAŽBA NA TERČÍCH	H	viz fasáda	
	BYTOVÁ JEDNOTKA č. 49	(plocha : 31,55 m2 + balkon 5,20 m2)				
650	PŘEDSÍŇ, KUCHYNĚ	8,40	VINYL tl. 3 mm (lepený)	G	VOS, MJB	
651	KOUPELNA	3,85	KERAMICKÁ DLAŽBA	F	VOS, MJB, PO, SDK	SDK s.v. 2350 mm PO v. 2350 mm
652	WC	1,50	KERAMICKÁ DLAŽBA	F	VOS, MJB, PO, SDK	SDK s.v. 2350 mm PO v. 2350 mm
653	POKOJ + KK	17,80	VINYL tl. 3 mm (lepený)	G	VOS, MJB	
654	BALKON	5,20	DLAŽBA NA TERČÍCH	H	viz fasáda	
	BYTOVÁ JEDNOTKA č. 50	(plocha : 31,80 m2 + balkon 6,90 m2)				
655	PŘEDSÍŇ, KUCHYNĚ	8,75	VINYL tl. 3 mm (lepený)	G	VOS, MJB	
656	KOUPELNA	3,90	KERAMICKÁ DLAŽBA	F	VOS, MJB, PO, SDK	SDK s.v. 2350 mm PO v. 2350 mm
657	WC	1,50	KERAMICKÁ DLAŽBA	F	VOS, MJB, PO, SDK	SDK s.v. 2350 mm PO v. 2350 mm
658	POKOJ + KK	17,65	VINYL tl. 3 mm (lepený)	G	VOS, MJB	
659	BALKON	6,90	DLAŽBA NA TERČÍCH	H	viz fasáda	
660	BALKON	4,50	DLAŽBA NA TERČÍCH	H	viz fasáda	

POZNÁMKA: VOS VÁPENNÁ OMÍTKA ŠTUKOVÁ MJB MALBA JEDNOBAREVNÁ BÍLÁ PO PÓROVINOVÝ OBKLAD SDK SÁDROKARTONOVÝ PODHLED (7/T) TH PODHLED THERMATEX 600/600 mm (8/T)

LEGENDA ZDIVA 6. NP

▨ ŽELEZOBETONOVÉ MONOLITICKÉ NOSNÉ KONSTRUKCE (sloupy ø500, 400/400 mm, pilíře, stropní desky, ztužující stěny, opěrné stěny, výtahová šachta) SOUČÁST STATICKÉ ČÁSTI DOKUMENTACE

▨ ODBODOVÉ VÝPLŇOVÉ ZDIVO Z BROUŠENÝCH BLOKŮ POROTHERM 30 PROFI (247x300x249 mm) tl. 300 mm PEVNOSTI P15 VYZDÍVANÉ NA MALTU PRO TENKÉ SPÁRY (na zdivu proveden kontaktní zateplovací systém s min. vlnou tl. 200 mm, ostění otvorů zatepleno min. vlnou tl. min. 30 mm)

◎ ZAŘÍZENÍ AUTONOMNÍ DETEKCE a SIGNALIZACE POŽÁRU (dle PBŘ stavby)

▨ MEZIBYTOVÉ STĚNY Z BLOKŮ Cihla Porotherm 25 AKU SYM – Akustická P 15 (rozměr 372 x 238 x 250 mm) tl. 250 mm, akustický cihelný blok s maltovou kapsou pro tl. stěny 25 cm na maltu M 10. Cihly jsou velmi vhodné pro mezibytové příčky tloušťky 250 mm. ZVUKOVÁ IZOLACE ZDIVA Rw = 57 dB (plošná hm. zdiva včetně omítek min. 313 kg/m2)

▨ ZDIVO PŘÍČEK Z PŘÍČKOVEK PORFIX TL. 100 mm a 150 mm VYZDÍVANÉ NA TMEL PORFIX (příčky, přizdívky), OMÍTKY VYZTUŽIT PERLINKOU

POZNÁMKA :

STROPY V OBYTNÝCH I NEOBYTNÝCH MÍSTNOSTECH BYTOVÝCH JEDNOTEK MOHOU BÝT OPATŘENY SDK PODHLEDY na s.v. 2,54 m (DLE VYHL. 146/2024 SB. min s.v. = 2,50 m)

SEZNAM STAVEBNÍCH ÚPRAV :

Ⓧ DECENTRÁLNÍ VĚTRACÍ REKUPERAČNÍ SYSTÉM se ZPĚTNÝM ZISKEM TEPLA (určený pro použití do prostorů s exponovaným venkovním hlukem) např. A–INVENT iV 14 – Zero, průměr otvoru 225 mm, tl. zdiva min. 255 mm, rozměr průchodky Ø 200 x 495/745 mm, průtok vzduchu v režimu zpětný zisk tepla 8,5–29 m3/h, hladina akustického tlaku (hlučnost) ve 2 m 10–31 dB(A) – 7 ks/patro

○ MŘÍŽKY DO DVEŘÍ 400/80 mm vřezané ke spodní hraně dveří (v místnostech sociálních zařízení s podtlakovým větráním) -12/T

±0,000 = PODLAHA 1. NP = 183,960 m.n.m., výškový systém B.p.V.

ZMĚNA STAVBY PŘED DOKONČENÍM č. 1

VEDOUCÍ PROJEKTANT	VYPRACOVAL	OBJEKT SO-101 APARTMÁNOVÝ-bytový DŮM	PROJEKTOVÁ KANCELÁŘ FABEDI s.r.o. Nám.3. května 1605 765 02 Otrokovice IČ: 116 78 852
ING. ARCH. RADKO PAVLACKÝ	ING. MICHAL NÁJEMNÍK		

INVESTOR: KŘETÍNSKÝ INVEST s.r.o., nám. 3. května 1820, 765 02 Otrokovice, IČO: 037 96 884

APARTMÁNOVÝ - BYTOVÝ DŮM V OTROKOVICÍCH
parc. č.st. 2120, 439/175, 439/117, 439/88, k.ú. Otrokovice

D.1.1 – ARCHITEKTONICKO – STAVEBNÍ ŘEŠENÍ

DATUM	09. 2026
FORMÁT	10 x A4
STUPEŇ	ZSD č. 1
ZAK. ČÍSLO	25 – 01
MĚŘÍTKO	1 : 50

PŮDORYS 6. NP ZSD č. 1 D 1.1 101/10