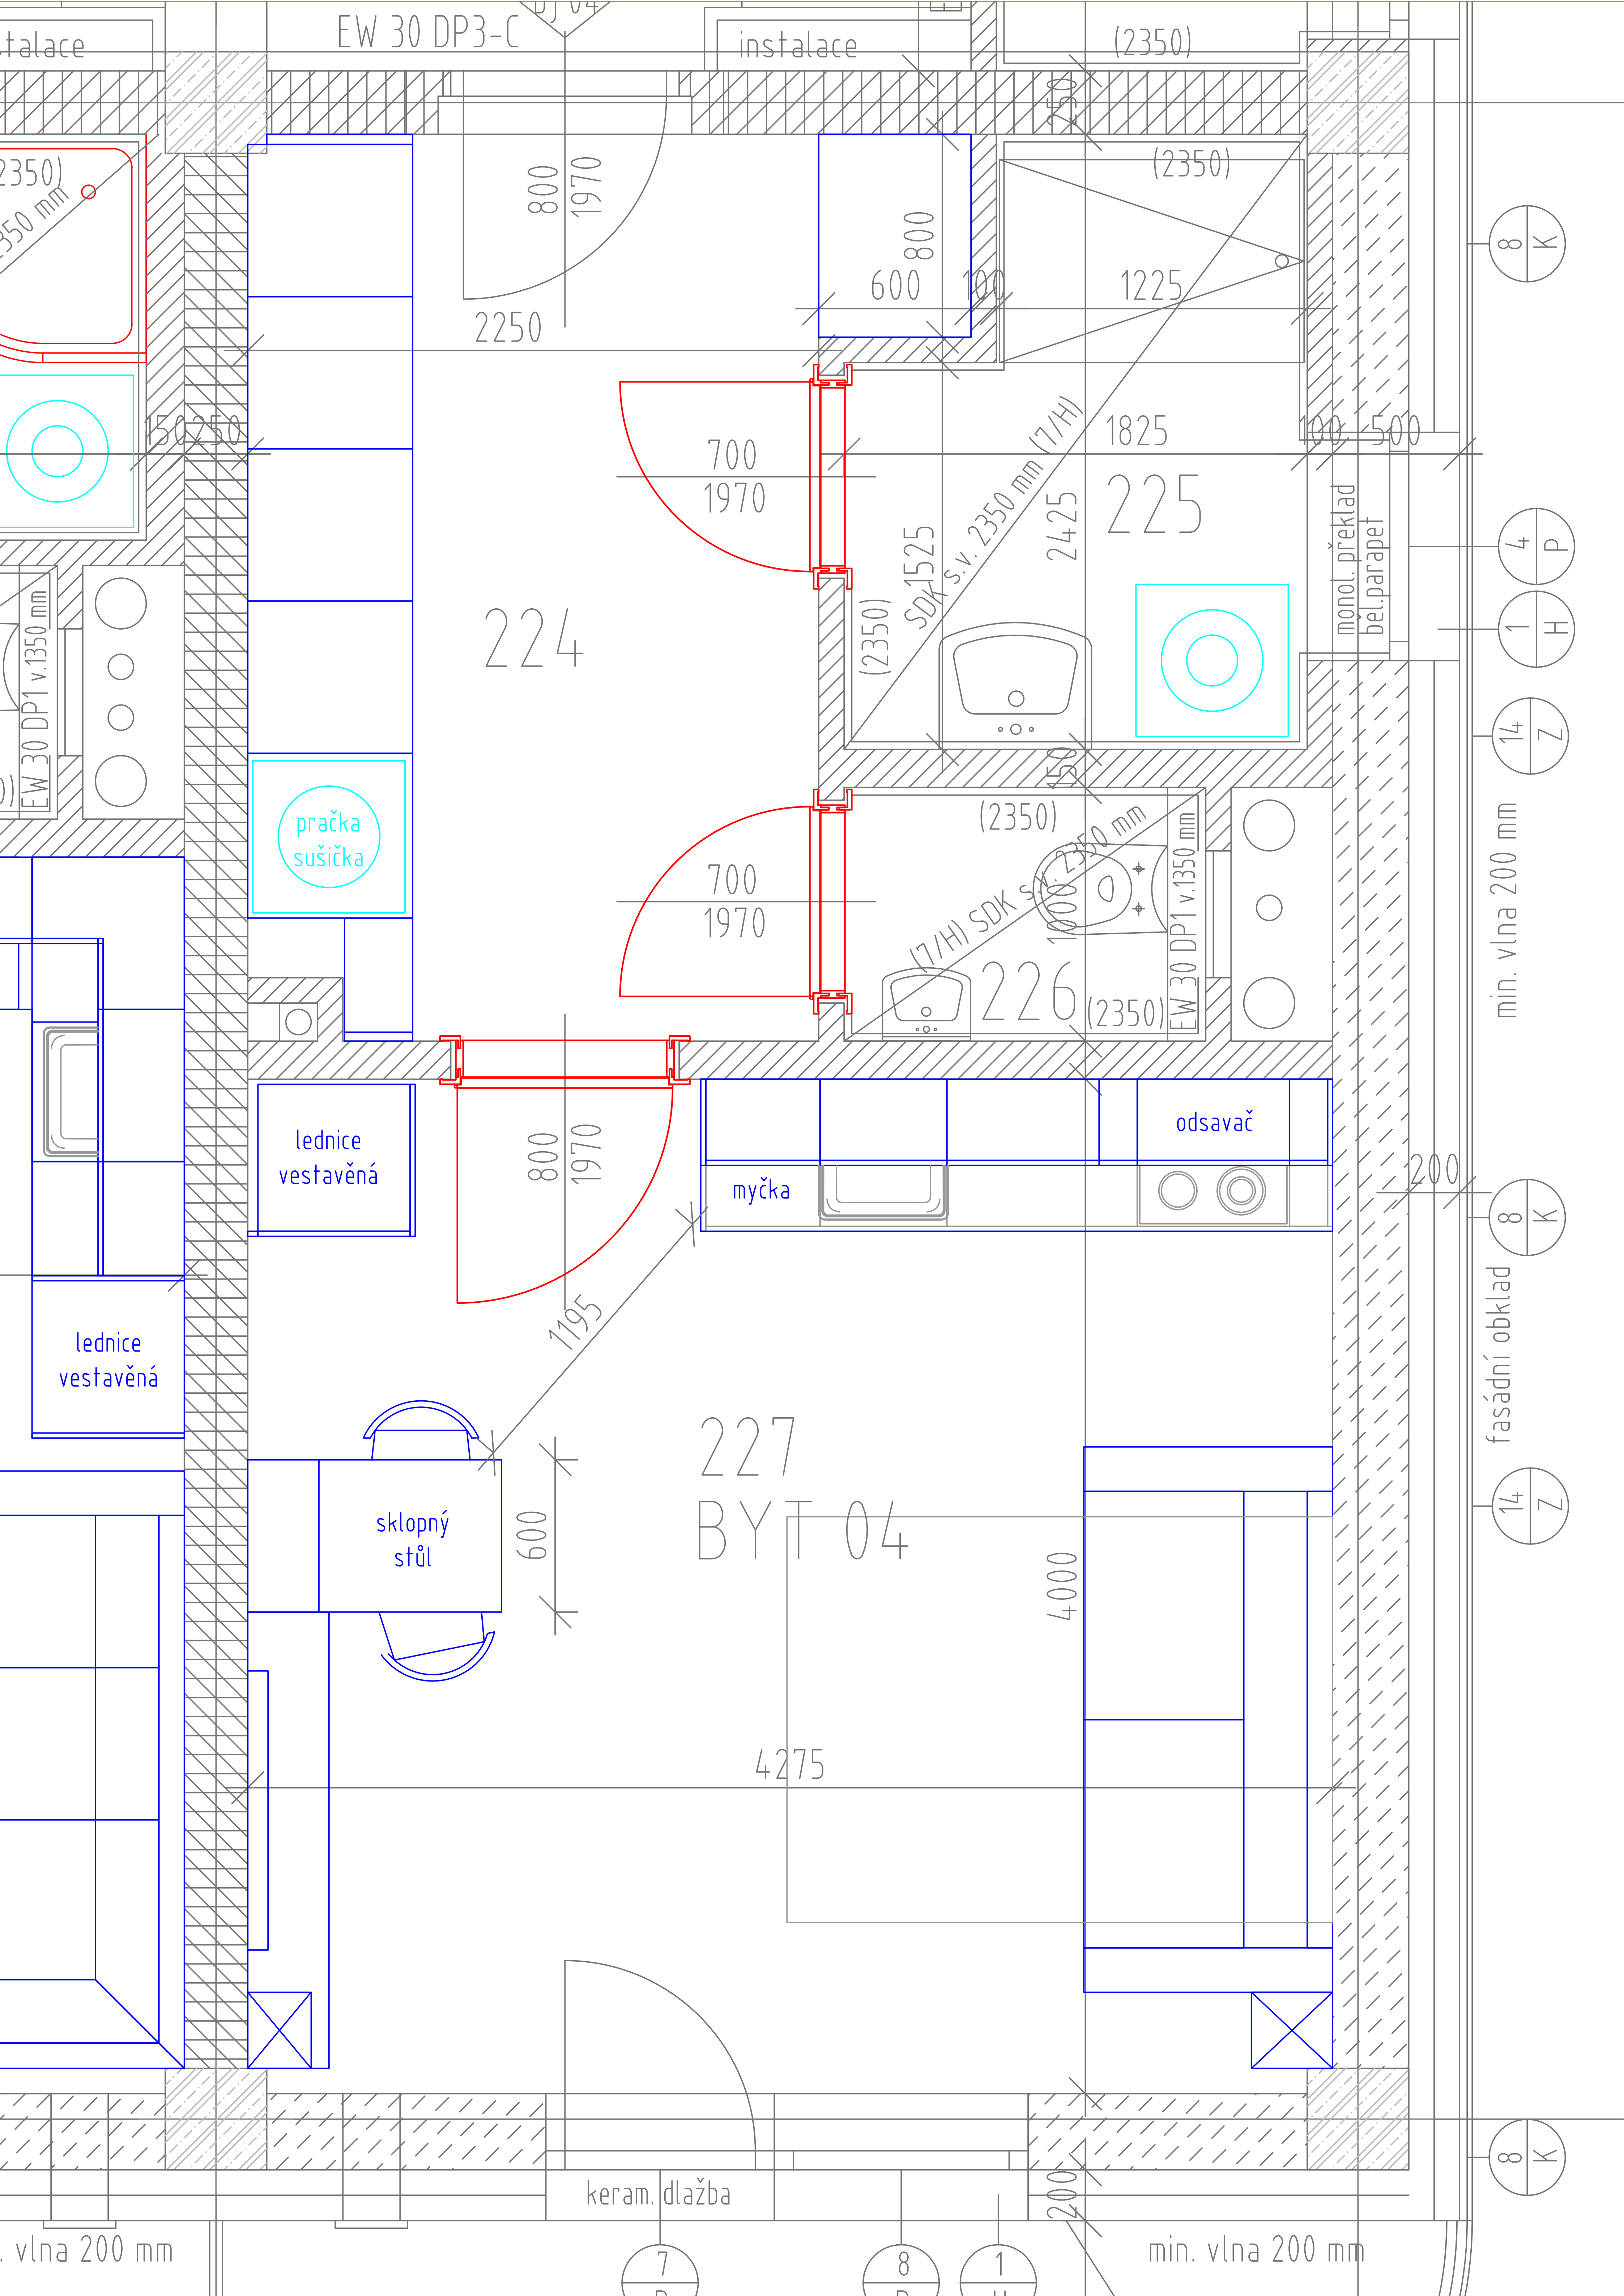
talace
EW 30 DP3-C
DJ 04
instalace
(2350)
250
(2350)
350 mm
800
1970
2250
800
600
100
1225
150 250
700
1970
1825
100
500
225
2425
SDK s.v. 2350 mm (7/H)
1525
(2350)
monol. překlad
bel.parapet
8
K
4
P
1
H
14
Z
224
EW 30 DP1 v.1350 mm
pračka
sušička
150
(2350)
(7/H) SDK s.v. 2350 mm
1000
700
1970
226
(2350)
EW 30 DP1 v.1350 mm
min. vlna 200 mm
lednice
vestavěná
800
1970
odsavač
myčka
200
8
K
1195
lednice
vestavěná
fasádní obklad
14
Z
227
BYT 04
sklopný
stůl
600
4000
4275
8
K
keram. dlažba
200
vlna 200 mm
min. vlna 200 mm
7
P
8
P
1
H